This drawing is the property of TNRIDC and L&T Construction,Transportation Infrastructure and must not be passed on to any person or body not authorised by us to receive it nor be copied or otherwise made use either in full or in part by suchperson or body without our prior permission in writing.

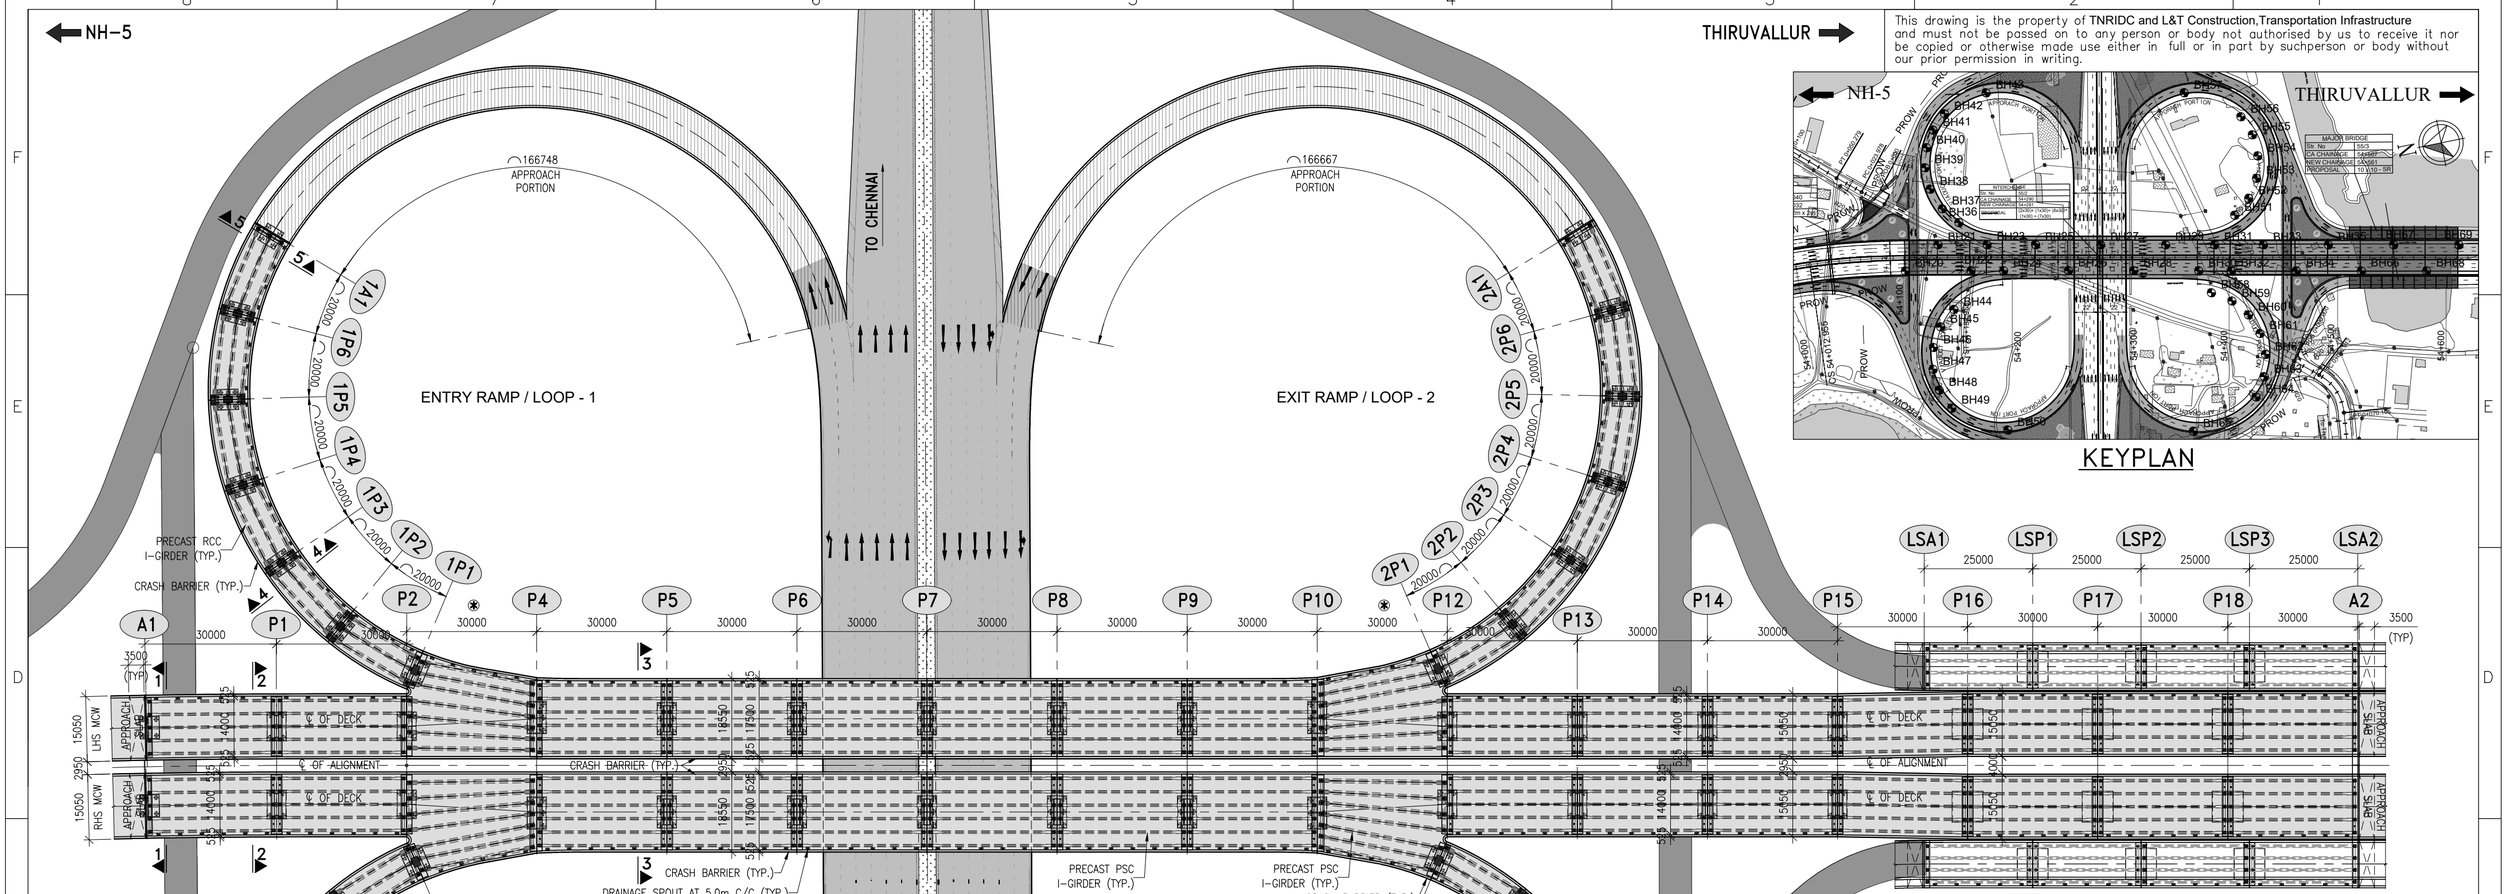

This drawing is the property of TNRIDC and L&T Construction,Transportation Infrastructure and must not be passed on to any person or body not authorised by us to receive it nor be copied or otherwise made use either in full or in part by suchperson or body without our prior permission in writing.

NH-5 ← THIRUVALLUR →

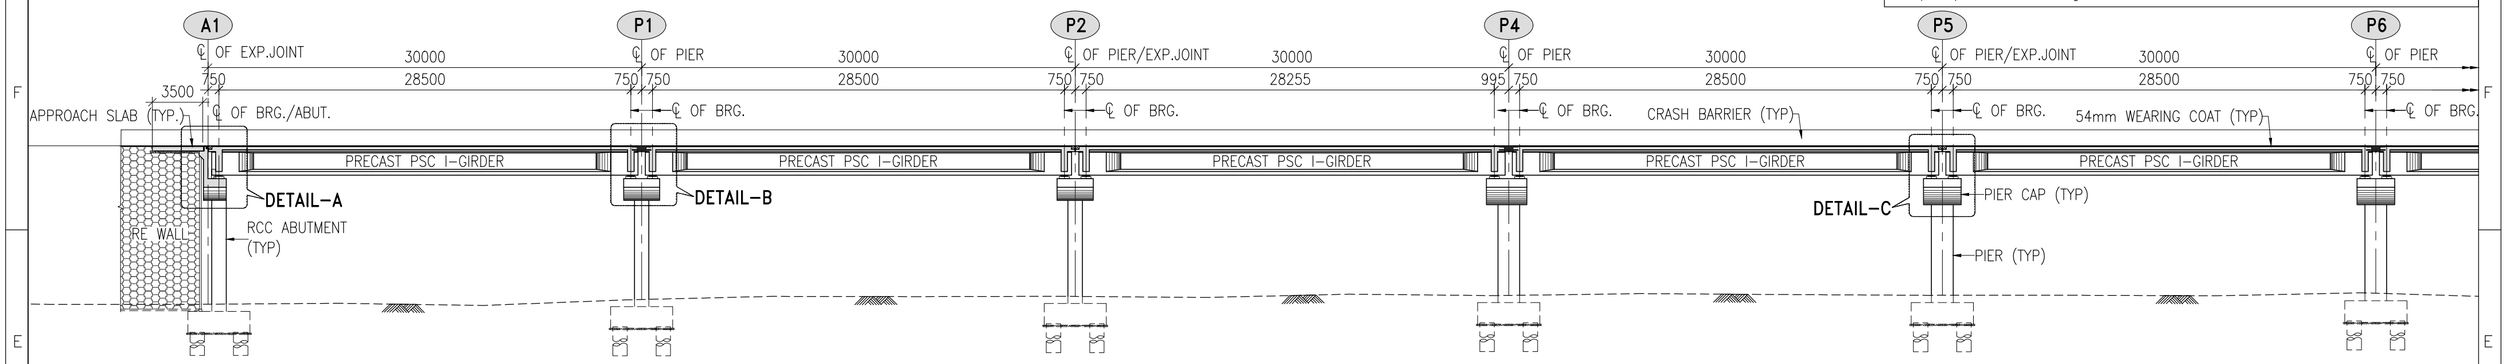

	LHS	RHS	LHS	RHS	LHS	RHS	LHS	RHS	LHS	RHS	LHS	RHS
FINISHED ROAD LEVEL (MCW)	52.003	52.003	52.003	52.003	52.003	52.003	52.003	52.003	52.003	52.003	52.003	52.003
GROUND LEVEL (MCW)	41.432	41.004	40.975	40.987	41.604	41.198	41.045	41.562	40.908	40.908	41.787	41.743
PILE CAP TOP LEVEL (MCW)	40.932	40.504	40.475	40.487	41.104	40.698	40.545	41.062	40.408	40.408	41.287	41.243
CAMBER (SLOPE)-e%	+1.86	-2.50	+0.79	-2.50	-0.29	-2.50	-1.36	-2.50	-2.42	-2.50	-2.50	-2.50
CHAINAGE	54+101	54+101	54+131	54+131	54+161	54+161	54+191	54+191	54+221	54+221	54+251	54+251

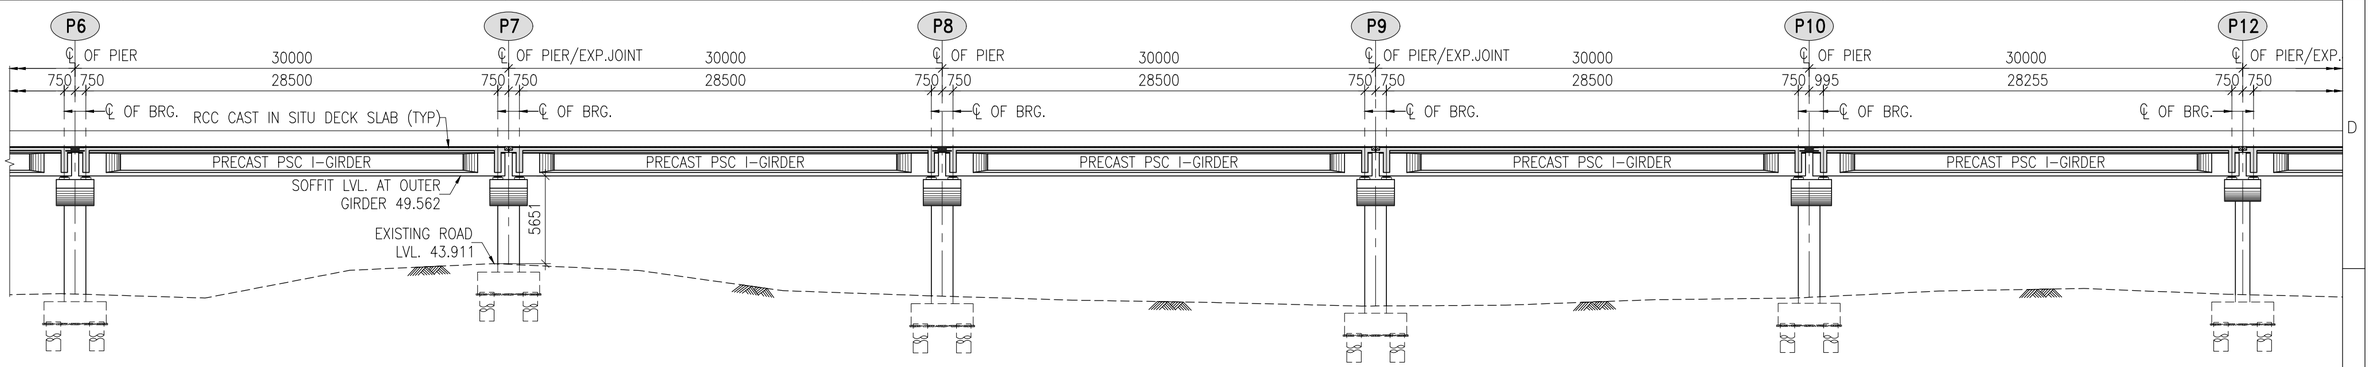

	LHS	RHS	LHS	RHS	LHS	RHS	LHS	RHS	LHS	RHS	LHS	RHS
FINISHED ROAD LEVEL (MCW)	52.003	52.003	52.003	52.003	52.003	52.003	52.003	52.003	52.003	52.003	52.003	52.003
GROUND LEVEL (MCW)	41.787	41.743	43.850	43.832	41.234	41.234	41.170	41.170	41.747	41.273	41.157	42.194
PILE CAP TOP LEVEL (MCW)	41.287	41.243	43.350	43.332	40.734	40.734	40.670	40.670	41.247	40.773	40.657	41.694
CAMBER (SLOPE)-e%	-2.50	-2.50	-2.50	-2.50	-2.50	-2.50	-2.50	-2.50	-2.50	-2.50	-2.50	-2.50
CHAINAGE	54+251	54+251	54+281	54+281	54+311	54+311	54+341	54+341	54+371	54+371	54+401	54+401

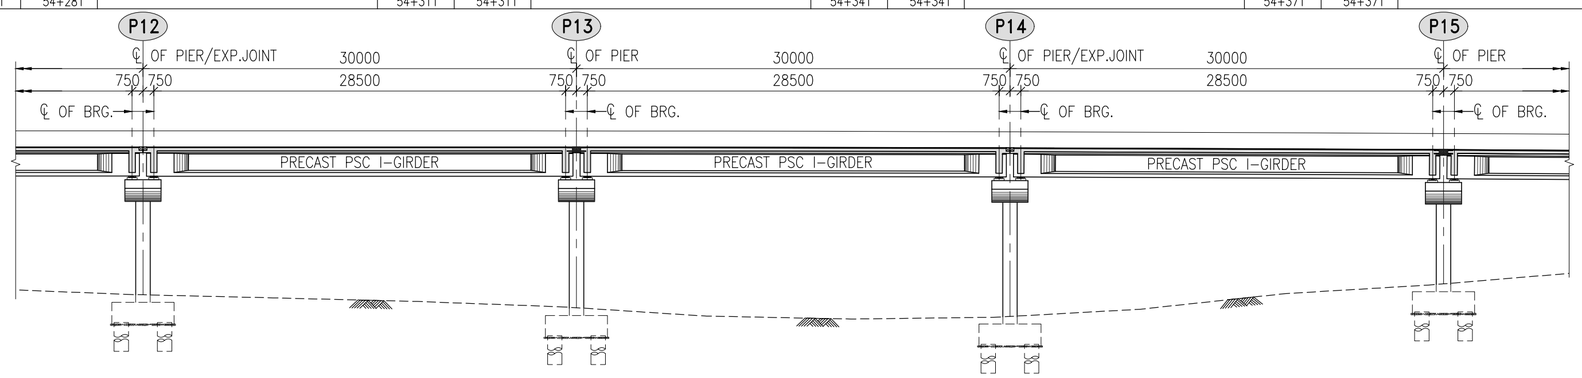

	LHS	RHS	LHS	RHS	LHS	RHS	LHS	RHS
FINISHED ROAD LEVEL (MCW)	52.003	52.003	51.999	51.999	51.943	51.943	51.821	51.821
GROUND LEVEL (MCW)	41.157	42.194	40.941	40.941	38.600	38.600	40.500	40.470
PILE CAP TOP LEVEL (MCW)	40.657	41.694	40.441	40.441	38.100	38.100	40.000	39.970
CAMBER (SLOPE)-e%	-2.50	-2.50	-2.50	-2.50	-2.50	-2.50	-2.50	-2.50
CHAINAGE	54+401	54+401	54+431	54+431	54+461	54+461	54+491	54+491

THIS DRAWING SHALL BE READ IN CONJUNCTION WITH DRAWING NO. O24087-C-RP-MB-GA-8330 (SHEET 1 OF 10)

LONGITUDINAL ELEVATION (MAIN CARRIAGEWAY) (SCALE 1:300)

FOR APPROVAL

REV	DATE	DESCRIPTION	DESIGNED	DRAWN	CHECKED	APPROVED
RC	08.10.25	REVISED BASED ON SITE CONDITION	SSR	SR	ARS	NKC
RB	18.09.25	REVISED AS PER IIT COMMENTS	SSR	SR	ARS	NKC
RA	14.08.25	FOR APPROVAL	SSR	SR	ARS	NKC

CLIENT : TNRIDC
TAMILNADU ROAD INFRASTRUCTURE DEVELOPMENT CORPORATION

AUTHORITY'S ENGINEER : THEME ENGINEERING SERVICE PVT. LTD.,

PROOF CONSULTANT : ASIA INFRASTRUCTURE ADVISORY SERVICES PRIVATE LIMITED

SAFETY CONSULTANT : ALMONDZ GLOBAL INFRA - CONSULTANT LIMITED (A wholly owned Subsidiary of AGSL)

CONTRACTOR : L&T Construction, Transportation Infrastructure

DESIGN CONSULTANT : L&T Construction, Transportation Infrastructure, EDRC

PROJECT : FORMATION OF NEW SIX LANE ROAD FROM THIRUVALLUR BYPASS (DESIGN CHAINAGE: CH 47+800) TO VENGATHUR (DESIGN CHAINAGE: CH 58+200) WITH PAVED SHOULDERS AND TWO LANE SERVICE ROAD ON BOTH SIDES IN SECTION-3 OF CHENNAI PERIPHERAL RING ROAD PROJECT UNDER PACKAGE-3 ON ENGINEERING, PROCUREMENT AND CONSTRUCTION (EPC) MODE INCLUDING MAINTENANCE FOR 7 YEARS.

AUTHORITY'S ENGINEER | PROOF CONSULTANT | DESIGN DIRECTOR

JOB No. : O24087-C-RP

DESIGNED	SSR	
DRAWN	SR	
CHECKED	ARS	
APPROVED	NKC	
DATE	14.08.2025	SCALE AS SHOWN

TITLE : GENERAL ARRANGEMENT DRAWING FOR INTERCHANGE AT CH: 54+281

REV: RC
SIZE: A2

DRAWING NO : O 2 4 0 8 7 - C - R P - M B - G A - 8 3 3 0

SHEET: 02 OF 10

Cad File No: D:\CPRR-2\STRUCTURES\INTERCHANGE_MJB\ O24087-C-RP-MB-GA-8330-RC_Interchange at Ch-54+281.dwg

Plot Date: 17 October, 2025 - 5:09 PM

NH–5

THIRUVALLUR

This drawing is the property of **TNRIDC and L&T Construction,Transportation Infrastructure** and must not be passed on to any person or body not authorised by us to receive it nor be copied or otherwise made use either in full or in part by suchperson or body without our prior permission in writing.

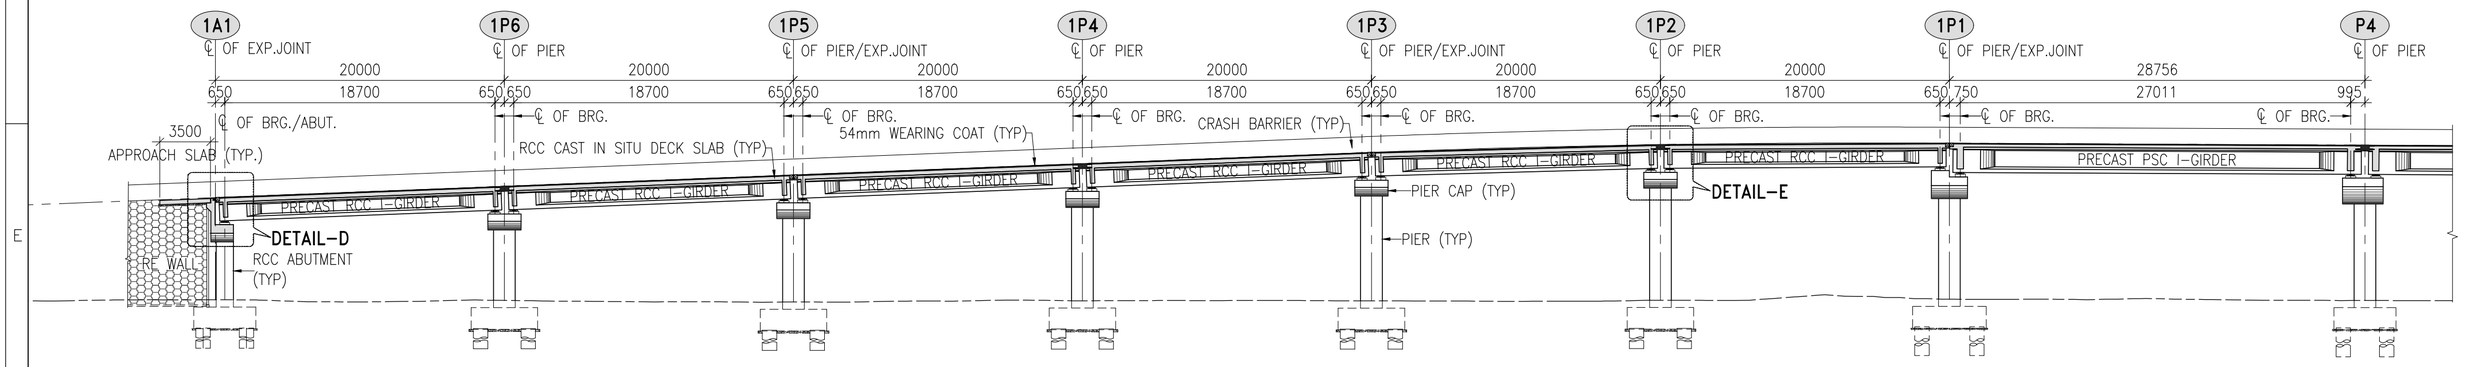

FINISHED ROAD LEVEL (LOOP)	48.179		48.961		49.744		50.526		51.307		51.844		51.943		52.003
GROUND LEVEL (LOOP)	41.102		41.059		40.952		41.036		41.029		40.090		41.140		41.045
PILE CAP TOP LEVEL (LOOP)	40.602		40.559		40.452		40.536		40.529		39.590		40.640		40.545
CAMBER (SLOPE)–e%	4.00		4.00		4.00		4.00		4.00		3.734		0.69		1.26
CHAINAGE	0+196.748		0+216.748		0+236.748		0+256.748		0+276.748		0+296.748		0+316.748		0+345.504

LONGITUDINAL ELEVATION (ENTRY RAMP/LOOP–1)

(SCALE 1:300)

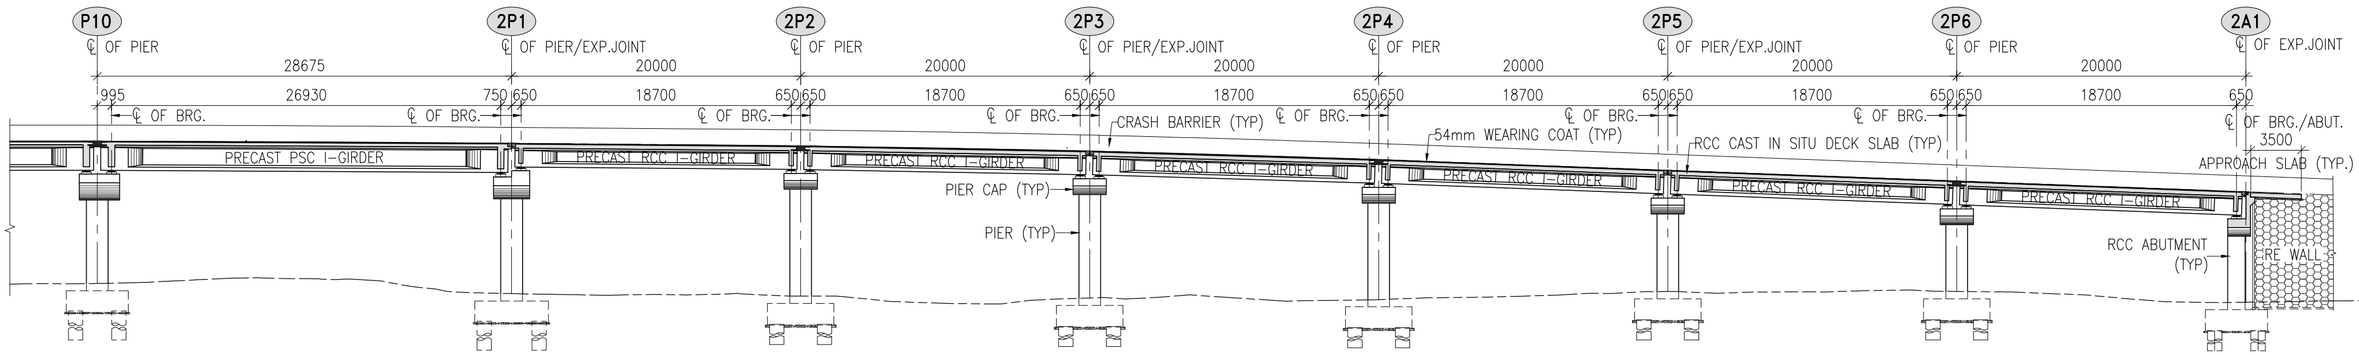

FINISHED ROAD LEVEL (LOOP)	52.003		51.500		51.320		50.962		50.373		49.633		48.890		48.146
GROUND LEVEL (LOOP)	41.747		41.098		40.927		40.795		38.840		40.313		40.313		40.497
PILE CAP TOP LEVEL (LOOP)	41.247		40.598		40.427		40.295		38.340		39.813		39.813		39.997
CAMBER (SLOPE)–e%	2.5		3.03		4.00		4.00		4.00		4.00		4.00		4.00
CHAINAGE	0+014.868		0+043.543		0+063.543		0+083.543		0+103.543		0+123.543		0+143.543		0+163.543

LONGITUDINAL ELEVATION (EXIT RAMP/LOOP–2)

(SCALE 1:300)

THIS DRAWING SHALL BE READ IN CONJUNCTION WITH DRAWING NO. O24087-C-RP-MB-GA-8330 (SHEET 1 OF 10)

FOR APPROVAL

REV	DATE	DESCRIPTION	DESIGNED	DRAWN	CHECKED	APPROVED
RC	08.10.25	REVISED BASED ON SITE CONDITION	SSR	SR	ARS	NKC
RB	18.09.25	REVISED AS PER IIT COMMENTS	SSR	SR	ARS	NKC
RA	14.08.25	FOR APPROVAL	SSR	SR	ARS	NKC

CLIENT : TNRIDC
TAMILNADU ROAD INFRASTRUCTURE DEVELOPMENT CORPORATION

AUTHORITY'S ENGINEER : THEME ENGINEERING SERVICE PVT. LTD.,

PROOF CONSULTANT : ASIA INFRASTRUCTURE ADVISORY SERVICES PRIVATE LIMITED

SAFETY CONSULTANT : ALMONDZ GLOBAL INFRA - CONSULTANT LIMITED (A wholly owned Subsidiary of AGSL)

PROJECT : FORMATION OF NEW SIX LANE ROAD FROM THIRUVALLUR BYPASS (DESIGN CHAINAGE: CH 47+800) TO VENGATHUR (DESIGN CHAINAGE: CH 58+200) WITH PAVED SHOULDERS AND TWO LANE SERVICE ROAD ON BOTH SIDES IN SECTION-3 OF CHENNAI PERIPHERAL RING ROAD PROJECT UNDER PACKAGE-3 ON ENGINEERING, PROCUREMENT AND CONSTRUCTION (EPC) MODE INCLUDING MAINTENANCE FOR 7 YEARS.

CONTRACTOR : L&T Construction, Transportation Infrastructure

DESIGN CONSULTANT : L&T Construction, Transportation Infrastructure, EDRC

AUTHORITY'S ENGINEER | PROOF CONSULTANT | DESIGN DIRECTOR

DESIGNED	SSR		
DRAWN	SR		
CHECKED	ARS		
APPROVED	NKC		
DATE	14.08.2025	SCALE	AS SHOWN

JOB No. : O24087-C-RP

TITLE : GENERAL ARRANGEMENT DRAWING FOR INTERCHANGE AT CH: 54+281

REV: RC

SIZE: A2

DRAWING NO : O 2 4 0 8 7 - C - R P - M B - G A - 8 3 3 0

SHEET: 03 OF 10

Cad File No: D:\CPRR-2\STRUCTURES\INTERCHANGE_MJB\ O24087-C-RP-MB-GA-8330-RC_Interchange at Ch-54+281.dwg

Plot Date: 17 October, 2025 - 5:10 PM

NH–5

THIRUVALLUR

This drawing is the property of TNRIDC and L&T Construction,Transportation Infrastructure and must not be passed on to any person or body not authorised by us to receive it nor be copied or otherwise made use either in full or in part by suchperson or body without our prior permission in writing.

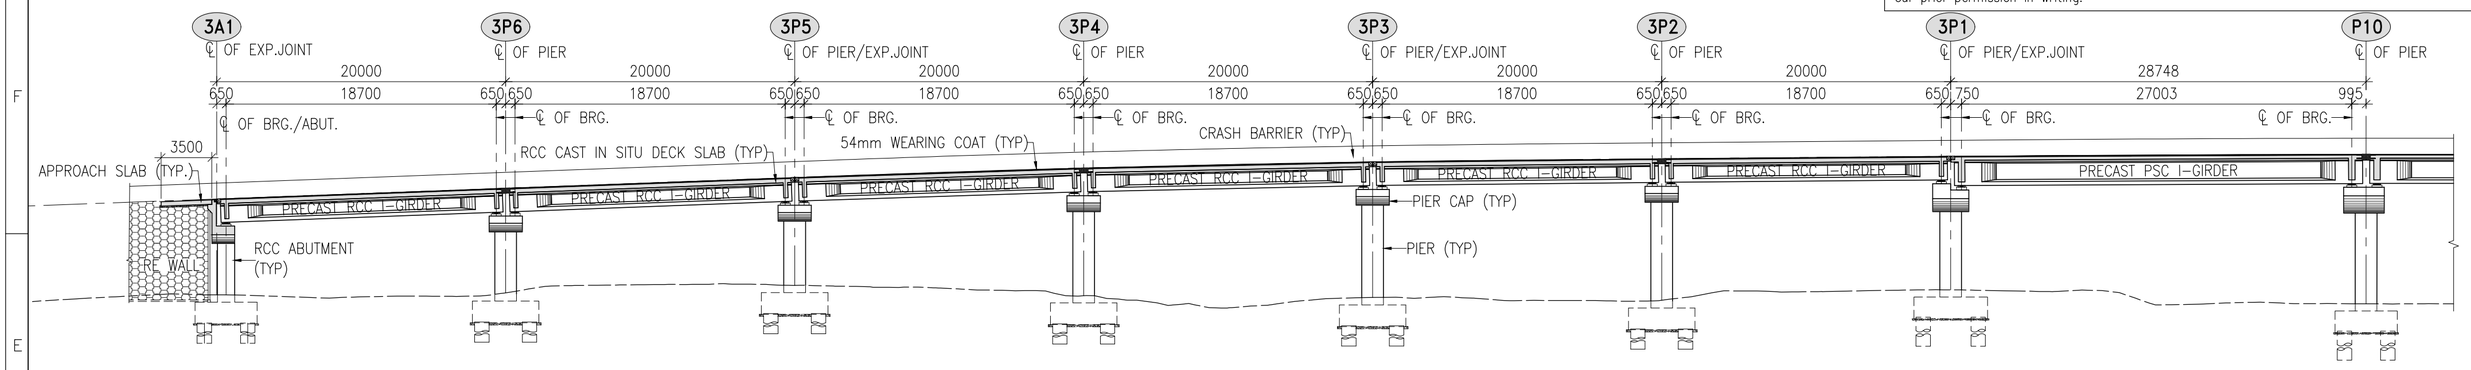

FINISHED ROAD LEVEL (LOOP)	48.551		49.295		50.039		50.695		51.123		51.337		51.506		52.003
GROUND LEVEL (LOOP)	**41.250**		**41.500**		**42.570**		**41.858**		**41.731**		**41.542**		**42.263**		**41.273**
PILE CAP TOP LEVEL (LOOP)	**40.750**		**41.000**		**42.070**		**41.358**		**41.231**		**41.042**		**41.763**		**40.773**
CAMBER (SLOPE)–e%	4.00		4.00		4.00		4.00		4.00		4.00		2.9		2.5
CHAINAGE	0+196.758		0+216.758		0+236.758		0+256.758		0+276.758		0+296.758		0+316.758		0+345.504

LONGITUDINAL ELEVATION (ENTRY RAMP/LOOP–3)

(SCALE 1:300)

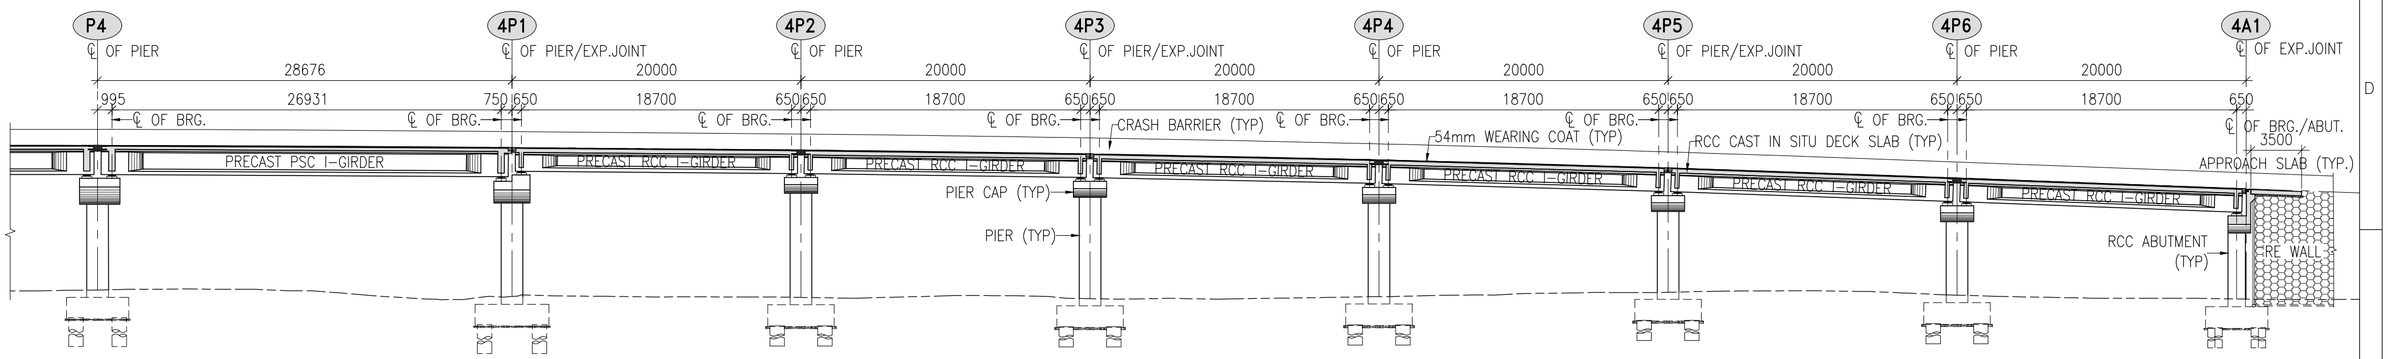

FINISHED ROAD LEVEL (LOOP)	52.003		51.499		51.328		51.060		50.648		50.091		49.392		48.646
GROUND LEVEL (LOOP)	**41.562**		**41.192**		**41.127**		**41.039**		**41.182**		**41.481**		**41.283**		**41.013**
PILE CAP TOP LEVEL (LOOP)	**41.062**		**40.692**		**40.627**		**40.539**		**40.682**		**40.981**		**40.783**		**40.513**
CAMBER (SLOPE)–e%	2.5		3.03		4.00		4.00		4.00		4.00		4.00		4.00
CHAINAGE	0+014.856		0+043.532		0+063.532		0+083.532		0+103.532		0+123.532		0+143.532		0+163.532

LONGITUDINAL ELEVATION (EXIT RAMP/LOOP–4)

(SCALE 1:300)

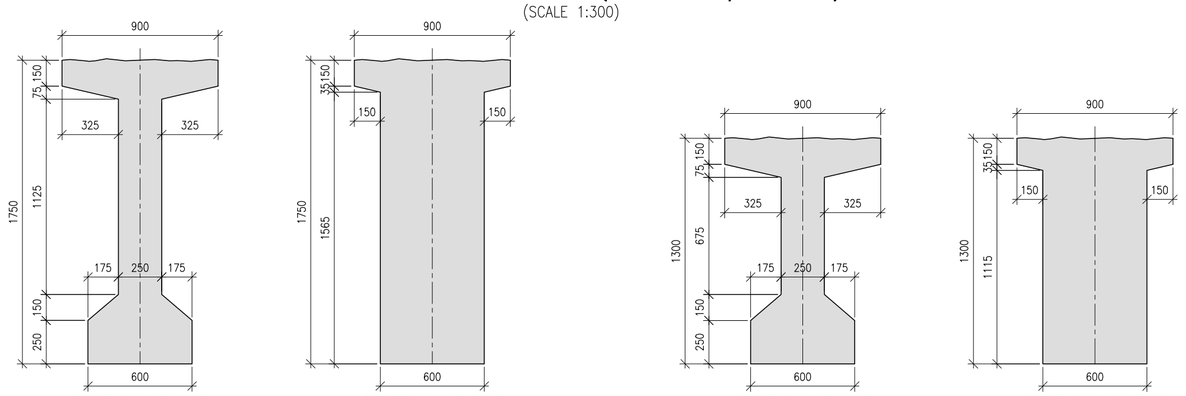

SECTION AT MID — SECTION AT END

DETAIL OF PSC GIRDER

(SCALE 1:25)

SECTION AT MID — SECTION AT END

DETAIL OF RCC GIRDER

(SCALE 1:25)

THIS DRAWING SHALL BE READ IN CONJUNCTION WITH DRAWING NO. O24087-C-RP-MB-GA-8330 (SHEET 1 OF 10)

FOR APPROVAL

REV	DATE	DESCRIPTION	DESIGNED	DRAWN	CHECKED	APPROVED
RC	08.10.25	REVISED BASED ON SITE CONDITION	SSR	SR	ARS	NKC
RB	18.09.25	REVISED AS PER IIT COMMENTS	SSR	SR	ARS	NKC
RA	14.08.25	FOR APPROVAL	SSR	SR	ARS	NKC

CLIENT : TNRIDC
TAMILNADU ROAD INFRASTRUCTURE DEVELOPMENT CORPORATION

AUTHORITY'S ENGINEER : TES THEME ENGINEERING SERVICE PVT. LTD.,

PROOF CONSULTANT : aip ASIA INFRASTRUCTURE ADVISORY SERVICES PRIVATE LIMITED

SAFETY CONSULTANT : almondz ALMONDZ GLOBAL INFRA - CONSULTANT LIMITED (A wholly owned Subsidiary of AGSL)

PROJECT : FORMATION OF NEW SIX LANE ROAD FROM THIRUVALLUR BYPASS (DESIGN CHAINAGE: CH 47+800) TO VENGATHUR (DESIGN CHAINAGE: CH 58+200) WITH PAVED SHOULDERS AND TWO LANE SERVICE ROAD ON BOTH SIDES IN SECTION-3 OF CHENNAI PERIPHERAL RING ROAD PROJECT UNDER PACKAGE-3 ON ENGINEERING, PROCUREMENT AND CONSTRUCTION (EPC) MODE INCLUDING MAINTENANCE FOR 7 YEARS.

CONTRACTOR : L&T Construction Transportation Infrastructure

DESIGN CONSULTANT : L&T Construction Transportation Infrastructure, EDRC

AUTHORITY'S ENGINEER | PROOF CONSULTANT | DESIGN DIRECTOR

ASIA INFRASTRUCTURE ADVISORY SERVICES PVT. LTD. — L&T CONSTRUCTION — Graduate DEC '3N DIRECTOR

JOB No. : O24087-C-RP

DESIGNED	SSR	
DRAWN	SR	
CHECKED	ARS	
APPROVED	NKC	
DATE	14.08.2025	SCALE AS SHOWN

TITLE : GENERAL ARRANGEMENT DRAWING FOR INTERCHANGE AT CH: 54+281

REV: RC

SIZE: A2

DRAWING NO : O 2 4 0 8 7 - C - R P - M B - G A - 8 3 3 0

SHEET: 04 OF 10

This drawing is the property of **TNRIDC and L&T Construction,Transportation Infrastructure** and must not be passed on to any person or body not authorised by us to receive it nor be copied or otherwise made use either in full or in part by suchperson or body without our prior permission in writing.

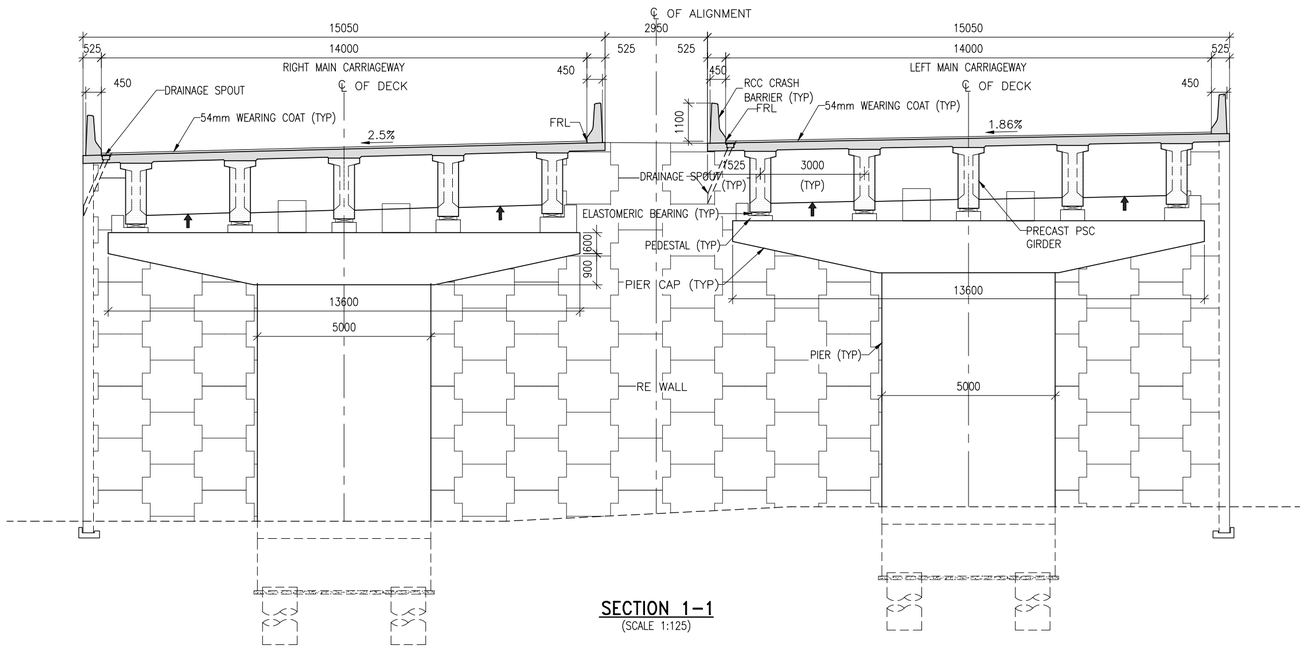

SECTION 1–1
(SCALE 1:125)

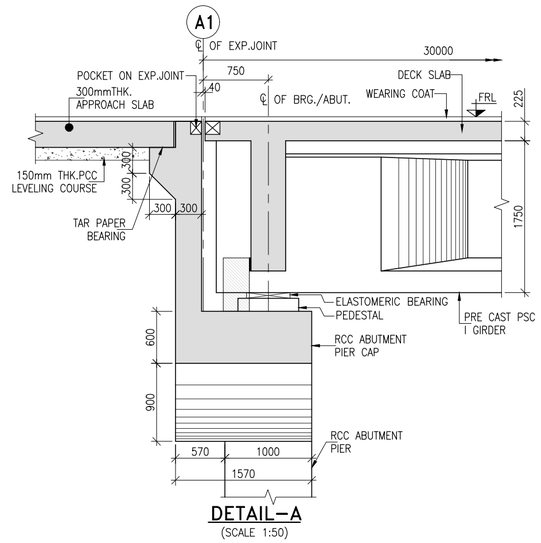

DETAIL–A
(SCALE 1:50)

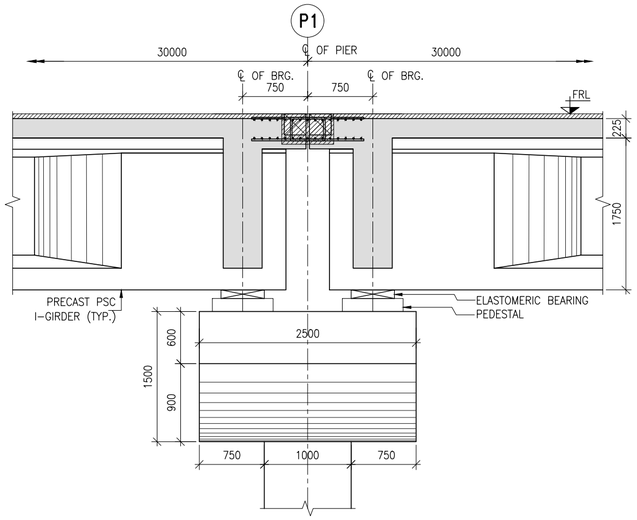

DETAIL–B
(SCALE 1:50)

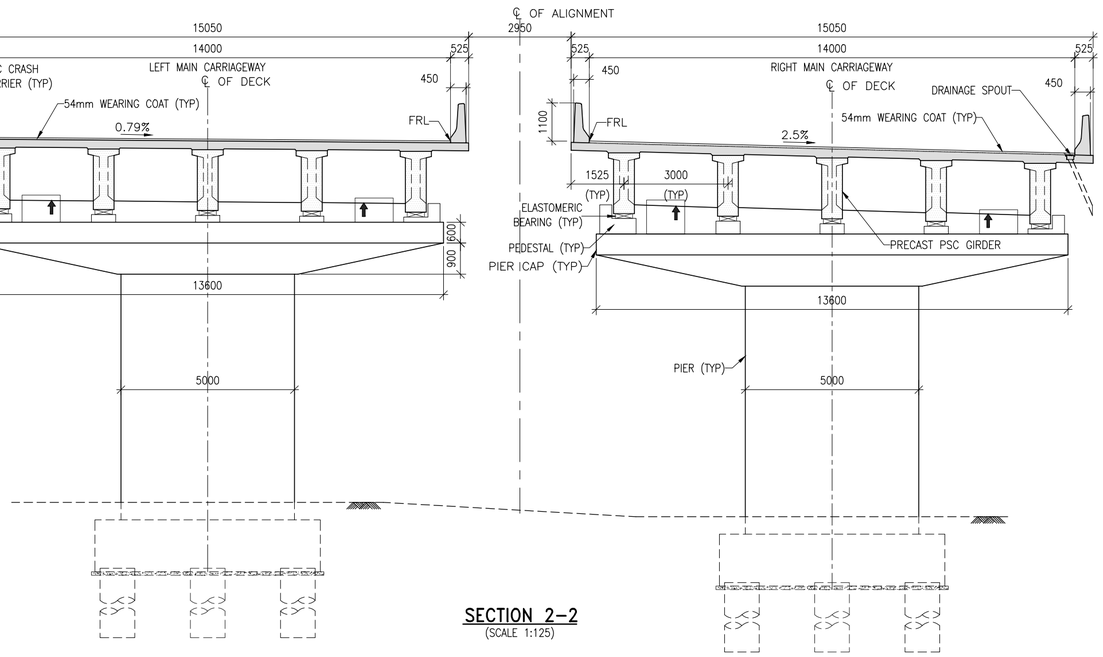

SECTION 2–2
(SCALE 1:125)

THIS DRAWING SHALL BE READ IN CONJUNCTION WITH DRAWING NO. O24087-C-RP-MB-GA-8330 (SHEET 1 OF 10)

FOR APPROVAL

REV	DATE	DESCRIPTION	DESIGNED	DRAWN	CHECKED	APPROVED
RC	08.10.25	REVISED BASED ON SITE CONDITION	SSR	SR	ARS	NKC
RB	18.09.25	REVISED AS PER IIT COMMENTS	SSR	SR	ARS	NKC
RA	14.08.25	FOR APPROVAL	SSR	SR	ARS	NKC

CLIENT :
TNRIDC
TAMILNADU ROAD INFRASTRUCTURE DEVELOPMENT CORPORATION

AUTHORITY'S ENGINEER :
THEME ENGINEERING SERVICE PVT. LTD.,

PROOF CONSULTANT :
ASIA INFRASTRUCTURE ADVISORY SERVICES PRIVATE LIMITED

SAFETY CONSULTANT :
ALMONDZ GLOBAL INFRA - CONSULTANT LIMITED
(A wholly owned Subsidiary of AGSL)

PROJECT :
FORMATION OF NEW SIX LANE ROAD FROM THIRUVALLUR BYPASS (DESIGN CHAINAGE: CH 47+800) TO VENGATHUR (DESIGN CHAINAGE: CH 58+200) WITH PAVED SHOULDERS AND TWO LANE SERVICE ROAD ON BOTH SIDES IN SECTION-3 OF CHENNAI PERIPHERAL RING ROAD PROJECT UNDER PACKAGE-3 ON ENGINEERING, PROCUREMENT AND CONSTRUCTION (EPC) MODE INCLUDING MAINTENANCE FOR 7 YEARS.

CONTRACTOR :
L&T Construction
Transportation Infrastructure

DESIGN CONSULTANT :
L&T Construction
Transportation Infrastructure, EDRC

AUTHORITY'S ENGINEER | **PROOF CONSULTANT** | **DESIGN DIRECTOR**

JOB No. : O24087-C-RP

DESIGNED	SSR	
DRAWN	SR	
CHECKED	ARS	
APPROVED	NKC	
DATE	14.08.2025	
SCALE	AS SHOWN	

TITLE :
GENERAL ARRANGEMENT DRAWING FOR INTERCHANGE AT CH: 54+281

REV: RC
SIZE: A2

DRAWING NO :
O 2 4 0 8 7 - C - R P - M B - G A - 8 3 3 0

SHEET: 05 OF 10

Cad File No: D:\CPRR-2\STRUCTURES\INTERCHANGE_MJB\ O24087-C-RP-MB-GA-8330-RC_Interchange at Ch-54+281.dwg

Plot Date: 17 October, 2025 - 5:12 PM

This drawing is the property of **TNRIDC and L&T Construction,Transportation Infrastructure** and must not be passed on to any person or body not authorised by us to receive it nor be copied or otherwise made use either in full or in part by suchperson or body without our prior permission in writing.

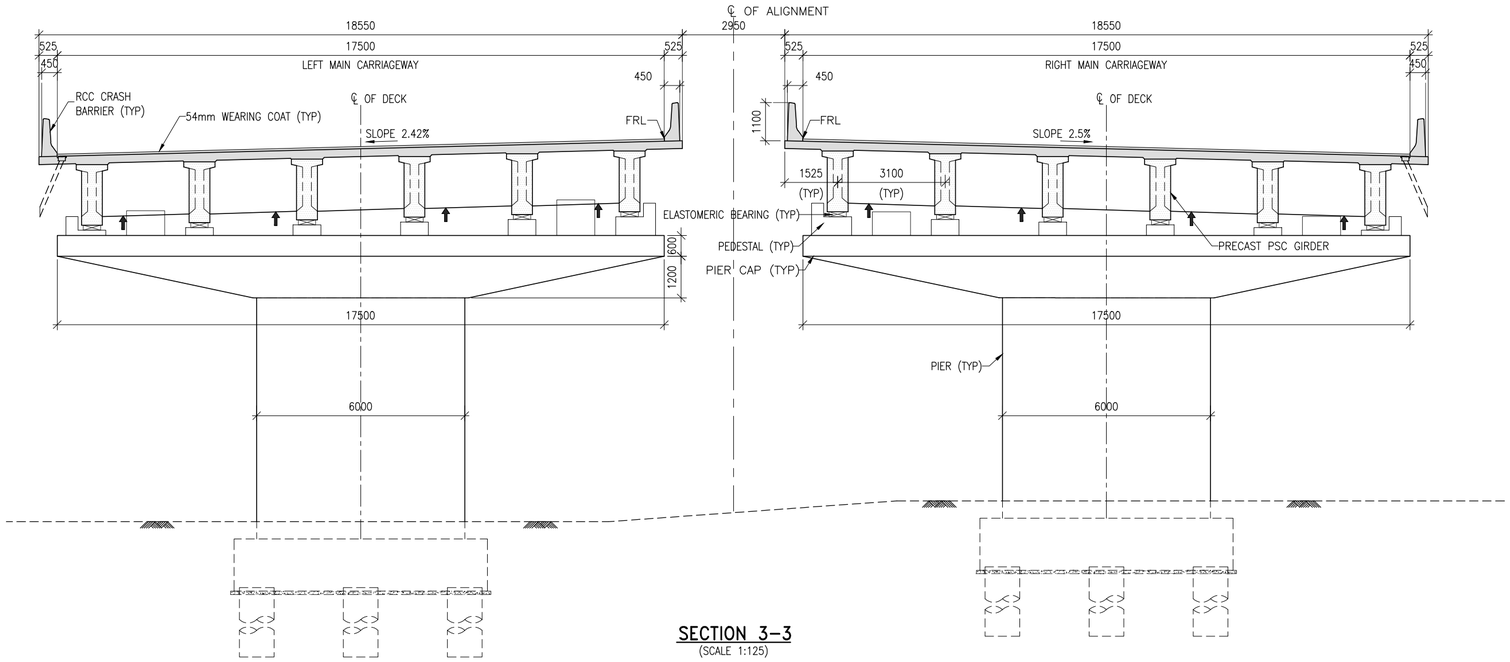

SECTION 3-3
(SCALE 1:125)

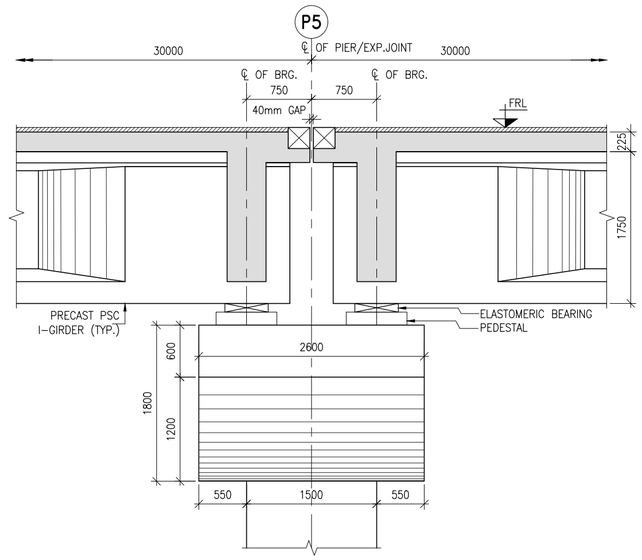

DETAIL-C
(SCALE 1:50)

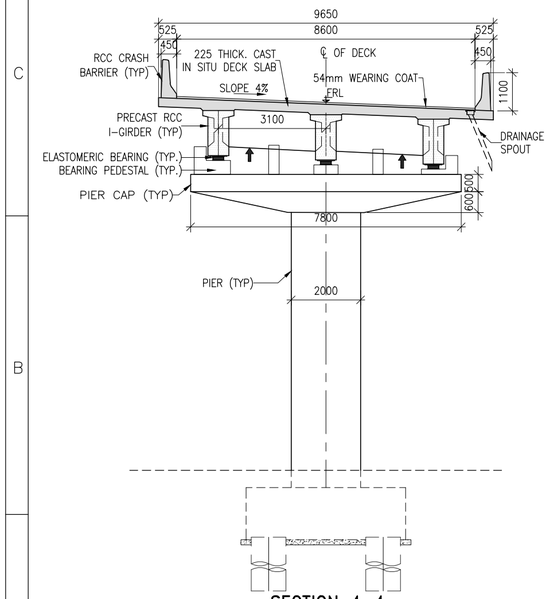

SECTION 4-4
(SCALE 1:125)

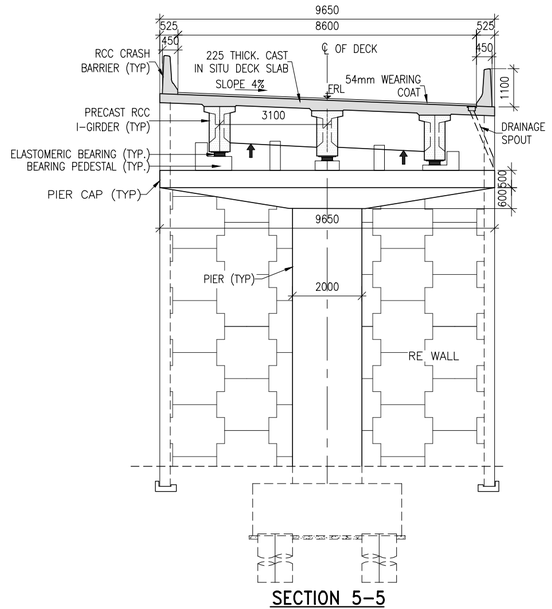

SECTION 5-5
(SCALE 1:125)

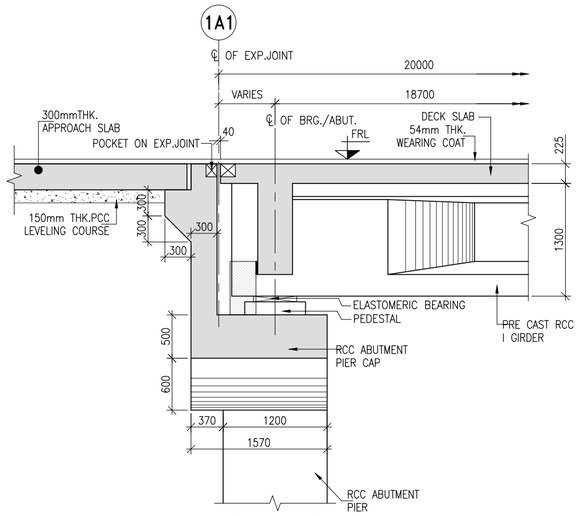

DETAIL-D
(SCALE 1:50)

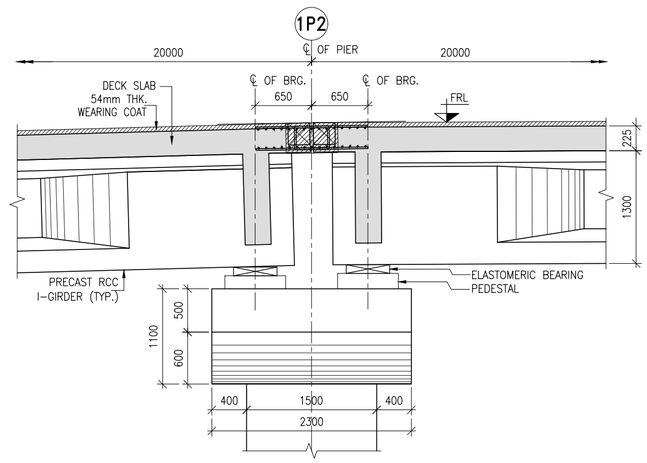

DETAIL-E
(SCALE 1:50)

THIS DRAWING SHALL BE READ IN CONJUNCTION WITH DRAWING NO. O24087-C-RP-MB-GA-8330 (SHEET 1 OF 10)

FOR APPROVAL

REV	DATE	DESCRIPTION	DESIGNED	DRAWN	CHECKED	APPROVED
RC	08.10.25	REVISED BASED ON SITE CONDITION	SSR	SR	ARS	NKC
RB	18.09.25	REVISED AS PER IIT COMMENTS	SSR	SR	ARS	NKC
RA	14.08.25	FOR APPROVAL	SSR	SR	ARS	NKC

CLIENT : TNRIDC
TAMILNADU ROAD INFRASTRUCTURE DEVELOPMENT CORPORATION

AUTHORITY'S ENGINEER : THEME ENGINEERING SERVICE PVT. LTD.,

PROOF CONSULTANT : ASIA INFRASTRUCTURE ADVISORY SERVICES PRIVATE LIMITED

SAFETY CONSULTANT : ALMONDZ GLOBAL INFRA - CONSULTANT LIMITED
(A wholly owned Subsidiary of AGSL)

PROJECT : FORMATION OF NEW SIX LANE ROAD FROM THIRUVALLUR BYPASS (DESIGN CHAINAGE: CH 47+800) TO VENGATHUR (DESIGN CHAINAGE: CH 58+200) WITH PAVED SHOULDERS AND TWO LANE SERVICE ROAD ON BOTH SIDES IN SECTION-3 OF CHENNAI PERIPHERAL RING ROAD PROJECT UNDER PACKAGE-3 ON ENGINEERING, PROCUREMENT AND CONSTRUCTION (EPC) MODE INCLUDING MAINTENANCE FOR 7 YEARS.

CONTRACTOR : L&T Construction, Transportation Infrastructure

DESIGN CONSULTANT : L&T Construction, Transportation Infrastructure, EDRC

AUTHORITY'S ENGINEER | PROOF CONSULTANT | DESIGN DIRECTOR

JOB No. : O24087-C-RP	
DESIGNED SSR	TITLE : GENERAL ARRANGEMENT DRAWING FOR INTERCHANGE AT CH: 54+281
DRAWN SR	REV: RC
CHECKED ARS	SIZE: A2
APPROVED NKC	DRAWING NO : O 2 4 0 8 7 - C - R P - M B - G A - 8 3 3 0
DATE 14.08.2025	SCALE AS SHOWN
	SHEET: 06 OF 10

Cad File No: D:\CPRR-2\STRUCTURES\INTERCHANGE_MJB\ O24087-C-RP-MB-GA-8330-RC_Interchange at Ch-54+281.dwg

Plot Date: 17 October, 2025 - 5:13 PM

This drawing is the property of TNRIDC and L&T Construction,Transportation Infrastructure and must not be passed on to any person or body not authorised by us to receive it nor be copied or otherwise made use either in full or in part by suchperson or body without our prior permission in writing.

DEPTH (m)	'N' VALUE	
0.00		
0.25	5	BROWNISH CLAYEY SAND (SC)
1.00	9	BROWNISH SILTY SAND (SP-SM)
2.00	14	BROWNISH SILTY SAND (SM)
3.00	15	BROWNISH SILTY SAND (SP-SM)
3.50		
4.00	18	BROWNISH SILTY SAND (SM)
5.00	19	BLACKISH SANDY CLAY (CI)
5.50		
6.00	23	GREYISH BROWN CLAYEY SAND (SC)
7.50	24	
9.00	25	
10.50	27	BROWNISH SILTY SAND (SM)
12.00	>100	GREYISH BROWN CLAYEY SAND (SC)
		HIGHLY WEATHERED ROCK
45.00		HIGHLY WEATHERED ROCK

BH-20-IN-54/29-01

DEPTH (m)	'N' VALUE	
0.00		
0.25	4	BROWNISH CLAYEY SAND (SC)
1.00	10	BROWNISH SILTY SAND (SM)
2.00	15	BROWNISH SILTY SAND (SP-SM)
3.00	11	
4.00	16	
5.00	8	GREYISH SILTY CLAY (CH)
6.00	18	GREYISH BROWN CLAYEY SAND (SC)
7.50	21	
9.00	22	
10.50	>100	BROWNISH, COMPLETELY WEATHERED, DISINTEGRATED SANDSTONE FRAGMENTS - INTERMEDIATE GEOMATERIAL
12.00	>100	GREYISH BROWN, COMPLETELY WEATHERED, DISINTEGRATED SANDSTONE FRAGMENTS - INTERMEDIATE GEOMATERIAL
13.50	>100	HIGHLY WEATHERED ROCK
		HIGHLY WEATHERED ROCK
45.00		

BH-21-IN-54/29-02

DEPTH (m)	'N' VALUE	
0.00		
0.25	7	BROWNISH CLAYEY SAND (SC)
1.00	14	BROWNISH SANDY CLAY (CI)
2.00	16	BROWNISH SILTY SAND (SM)
3.00	21	
4.00	20	
5.00	22	GREYISH CLAYEY SAND (SC)
6.00	10	GREYISH BROWN CLAYEY SAND (SP-SM)
7.50	27	GREYISH CLAYEY SAND WITH CALCAREOUS MATERIALS (SC)
9.00	31	
10.50	48	GREYISH BROWN CLAYEY SAND WITH SANDSTONE FRAGMENTS
12.00	>100	BROWNISH, COMPLETELY WEATHERED, DISINTEGRATED SANDSTONE FRAGMENTS - INTERMEDIATE GEOMATERIAL
13.50	>100	HIGHLY WEATHERED ROCK
		HIGHLY WEATHERED ROCK
45.00		

BH-22-IN-54/29-03

DEPTH (m)	'N' VALUE	
0.00		
0.25	7	BROWNISH SILTY SAND (SM)
1.00	11	BROWNISH CLAYEY SAND (SC)
2.00	12	BROWNISH SILTY SAND (SP)
3.00	13	
4.00	16	BROWNISH SILTY SAND (SM)
4.50		
5.00	20	BROWNISH GREY SANDY CLAY (CI)
6.00	23	
7.50	26	GREYISH BROWN CLAYEY SAND WITH CALCAREOUS DEPOSITS (SC)
9.00	38	
10.50	30	
12.00	>100	GREYISH BROWN CLAYEY SAND WITH SANDSTONE FRAGMENTS
		HIGHLY WEATHERED ROCK
45.00		HIGHLY WEATHERED ROCK

BH-23-IN-54/29-04

DEPTH (m)	'N' VALUE	
0.00		
0.25	4	BROWNISH CLAYEY SAND (SC)
1.00	10	BROWNISH SILTY SAND (SP-SM)
2.00	16	
3.00	18	
4.00	15	BROWNISH SILTY SAND (SP)
4.50		
5.00	8	GREYISH SANDY CLAY (CI)
6.00	28	BROWNISH GREY CLAYEY SAND (SC)
7.50	31	
9.00	34	
10.50	39	GREYISH BROWN CLAYEY SAND WITH CALCAREOUS DEPOSITS (SC)
12.00	>100	GREYISH BROWN CLAYEY SAND WITH SANDSTONE FRAGMENTS
		HIGHLY WEATHERED ROCK
45.00		HIGHLY WEATHERED ROCK

BH-24-IN-54/29-05

DEPTH (m)	'N' VALUE	
0.00		
1.00	9	WELL GRADED-SILTY SAND (SW-SM)
2.00	8	
3.00	10	
4.00	20	BROWNISH POORLY GRADED SAND (SP)
5.00	16	WELL GRADED-SILTY SAND (SW-SM)
6.00	15	
7.50	19	SANDY SILT (ML)
9.00	22	BROWN CLAYEY SAND (SC)
10.50	24	
12.00	27	
13.50	<100	
15.00	<100	BROWNISH SILTY SAND (SM)
16.50	<100	
18.00	<100	
19.50	<100	
21.00	103	
22.50	<100	
24.00	81	
25.50	<100	BROWNISH GREY SAND CLAY (CI)
27.00	87	SANDY SILT (ML)
28.50	<100	BROWNISH SANDY CLAY (CL)
30.00	<100	
34.50	<100	BROWNISH GREY SAND CLAY (CI)
36.00	<100	
39.00	<100	BROWNISH SILTY SAND (SM)
40.00		
40.50	<100	HIGHLY WEATHERED ROCK
45.00		HIGHLY WEATHERED ROCK

BH-29 (IN-54/29-10)

DEPTH (m)	'N' VALUE	
0.00		
0.25	4	BROWNISH CLAYEY SAND (SC)
1.00	5	BROWNISH SILTY SAND (SM)
2.00	10	BROWNISH SILTY SAND (SP-SM)
3.00	13	
4.00	14	
5.00	17	GREYISH CLAYEY SAND (SC)
6.00	20	
7.50	27	GREYISH BROWN SANDY CLAY WITH CALCAREOUS DEPOSITS (CI)
9.00	34	GREYISH BROWN CLAYEY SAND (SC)
10.50	40	GREYISH BROWN SANDY CLAY WITH CALCAREOUS DEPOSITS (CI)
12.00	>100	GREYISH BROWN CLAYEY SAND WITH SANDSTONE FRAGMENTS
		HIGHLY WEATHERED ROCK
45.00		HIGHLY WEATHERED ROCK

BH-25-IN-54/29-06

DEPTH (m)	'N' VALUE	
0.00		
0.25	6	BROWNISH CLAYEY SAND (SC)
1.00	7	
2.00	10	BROWNISH SILTY SAND (SP-SM)
3.00	15	
3.50		
4.00	17	BROWNISH SILTY SAND (SM)
5.00	20	BROWNISH SILTY SAND (SP-SM)
6.00	12	
6.50		
7.50	19	BROWNISH GREY CLAYEY SAND (SC)
9.00	17	
10.50	23	GREYISH BROWN SANDY CLAY WITH CALCAREOUS DEPOSITS (CL)
12.00	27	BROWNISH GREY CLAYEY SAND (SC)
13.50	24	
15.00	35	BROWNISH GREY SANDY CLAY (CI)
16.50	30	BROWNISH SILTY SAND (SM)
18.00	35	BROWNISH CLAYEY SAND WITH CALCAREOUS DEPOSITS (SC-CL)
19.50	>100	BROWNISH CLAYEY SAND WITH SANDSTONE FRAGMENTS
		HIGHLY WEATHERED ROCK
45.00		HIGHLY WEATHERED ROCK

BH-26-IN-54/29-07

DEPTH (m)	'N' VALUE	
0.00		
0.25	7	GREYISH CLAYEY SAND (SC)
1.00	8	
2.00	12	BROWNISH GREY SANDY CLAY (CI)
3.00	13	BROWNISH CLAYEY SAND (SC)
3.50		
4.00	13	BROWNISH GREY SILTY SAND (SM)
5.00	14	
5.50		BROWNISH SILTY SAND (SP - SM)
6.00	18	
7.50	20	
9.00	12	GREYISH SILTY CLAY (CH)
10.50	20	GREYISH SANDY CLAY (CI)
12.00	22	GREYISH CLAYEY SAND (SC)
13.50	28	BROWNISH GREY SANDY CLAY (CI) - WITH CALCAREOUS DEPOSITS
15.00	34	BROWNISH GREY CLAYEY SAND (SC) - WITH CALCAREOUS DEPOSITS
16.50	34	
18.00	>100	BROWNISH GREY CLAYEY SAND WITH SANDSTONE FRAGMENTS
		HIGHLY WEATHERED ROCK
45.00		HIGHLY WEATHERED ROCK

BH-27-IN-54/29-08

DEPTH (m)	'N' VALUE	
0.00		
1.00	7	BROWNISH CLAYEY SAND (SC)
2.00	10	BROWNISH SILTY SAND (SM)
3.00	12	BROWNISH SAND (SP)
4.00	13	
5.00	13	
6.00	16	
7.50	18	BROWNISH GREY CLAYEY SAND (SC)
9.00	27	GREYISH CLAYEY SAND WITH CALCAREOUS MATERIALS (SC)
10.50	33	BROWNISH GREY SANDY CLAY WITH CALCAREOUS MATERIALS (CI)
12.00	35	BROWNISH GREY CLAYEY SAND WITH CALCAREOUS MATERIALS (SC)
13.50	>100	BROWNISH, COMPLETELY WEATHERED, DISINTEGRATEDSANDSTONE FRAGMENTS - INTERMEDIATE GEOMATERIAL
		HIGHLY WEATHERED ROCK
45.00		HIGHLY WEATHERED ROCK

BH-28 (IN-54/29-10)

DEPTH (m)	'N' VALUE	
0.00		
1.00	7	BROWNISH SILTY SAND (SM)
2.00	11	
3.00	10	BROWNISH SAND (SP)
4.00	14	
5.00	16	
6.00	17	BROWNISH SILTY SAND (SM)
7.50	21	GREYISH BROWN CLAYEY SAND (SC)
9.00	28	
10.50	34	BROWNISH GREY CLAYEY SAND WITH CALCAREOUS MATERIALS (SC)
12.00	34	
13.50	38	
15.00	38	BROWNISH CLAYEY SAND (SC)
16.50	38	BROWNISH SILTY SAND WITH SANDSTONE FRAGMENTS
		HIGHLY WEATHERED ROCK
45.00		HIGHLY WEATHERED ROCK

BH-30 (IN-54/29-10)

LEGEND:

DF : DEPTH OF FOUNDATION FROM OGL
DGI : DEPTH OF PROPOSED GROUND IMPROVEMENT BELOW FOUNDATION

THIS DRAWING SHALL BE READ IN CONJUNCTION WITH DRAWING NO. O24087-C-RP-MB-GA-8330 (SHEET 1 OF 10)

FOR APPROVAL

REV	DATE	DESCRIPTION	DESIGNED	DRAWN	CHECKED	APPROVED
RB	18.09.25	REVISED AS PER IIT COMMENTS	SSR	SR	ARS	NKC
RA	14.08.25	FOR APPROVAL	SSR	SR	ARS	NKC

CLIENT : TNRIDC
TAMILNADU ROAD INFRASTRUCTURE DEVELOPMENT CORPORATION

AUTHORITY'S ENGINEER : TES THEME ENGINEERING SERVICE PVT. LTD.,

PROOF CONSULTANT : aip ASIA INFRASTRUCTURE ADVISORY SERVICES PRIVATE LIMITED

SAFETY CONSULTANT : almondz ALMONDZ GLOBAL INFRA - CONSULTANT LIMITED (A wholly owned Subsidiary of AGSL)

PROJECT : FORMATION OF NEW SIX LANE ROAD FROM THIRUVALLUR BYPASS (DESIGN CHAINAGE: CH 47+800) TO VENGATHUR (DESIGN CHAINAGE: CH 58+200) WITH PAVED SHOULDERS AND TWO LANE SERVICE ROAD ON BOTH SIDES IN SECTION-3 OF CHENNAI PERIPHERAL RING ROAD PROJECT UNDER PACKAGE-3 ON ENGINEERING, PROCUREMENT AND CONSTRUCTION (EPC) MODE INCLUDING MAINTENANCE FOR 7 YEARS.

CONTRACTOR : L&T Construction Transportation Infrastructure

DESIGN CONSULTANT : L&T Construction Transportation Infrastructure, EDRC

AUTHORITY'S ENGINEER | PROOF CONSULTANT | DESIGN DIRECTOR

JOB No. : O24087-C-RP

DESIGNED	SSR	
DRAWN	SR	
CHECKED	ARS	
APPROVED	NKC	
DATE	14.08.2025	
SCALE	AS SHOWN	

TITLE : INTERCHANGE AT CH:54+281
GENERAL ARRANGEMENT OF INTERCHANGE BORE LOG DETAILS

REV: RB
SIZE: A2

DRAWING NO : O 2 4 0 8 7 - C - R P - M B - G A - 8 3 3 0
SHEET: 07 OF 10

Cad File No: D:\CPRR-2\STRUCTURES\INTERCHANGE_MJB\ O24087-C-RP-MB-GA-8330-RC_Interchange at Ch-54+281.dwg

Plot Date: 17 October, 2025 - 5:14 PM

This drawing is the property of TNRIDC and L&T Construction,Transportation Infrastructure and must not be passed on to any person or body not authorised by us to receive it nor be copied or otherwise made use either in full or in part by suchperson or body without our prior permission in writing.

DEPTH (m)	'N' VALUE	
0.00		
0.25	4	GREYISH BROWN CLAYEY SAND (SC)
1.00	4	BROWNISH SILTY SAND (SM)
2.00	5	
3.00	11	GREYISH BROWN SILTY SAND (SP-SM)
4.00	9	
5.00	10	
6.00	14	
7.50	15	GREYISH BROWN CLAYEY SAND (SC)
9.00	16	
10.50	18	
12.00	20	
13.50	19	GREYISH BROWN CLAYEY SAND WITH CALCAREOUS DEPOSITS (SC)
15.00	>100	BROWNISH SANDY CLAY WITH SANDSTONE FRAGMENTS
		HIGHLY WEATHERED ROCK
45.00		HIGHLY WEATHERED ROCK

BH-31-IN-54/29-12

DEPTH (m)	'N' VALUE	
0.00		
0.25	5	GREYISH BROWN CLAYEY SAND (SC)
1.00	6	BROWNISH SILTY SAND (SM)
2.00	10	BROWNISH SAND (SP)
3.00	13	BROWNISH SILTY SAND (SM)
4.00	15	GREYISH BROWN SILTY SAND (SP-SM)
5.00	20	
6.00	21	
7.50	26	GREYISH BROWN CLAYEY SAND WITH CALCAREOUS DEPOSITS (SC)
9.00	18	
10.50	20	GREYISH BROWN CLAYEY SAND WITH CALCAREOUS DEPOSITS (SC-CI)
12.00	33	
13.50	37	GREYISH BROWN CLAYEY SAND WITH CALCAREOUS DEPOSITS (SC)
15.00	>100	BROWNISH CLAYEY SAND WITH SANDSTONE FRAGMENTS
		HIGHLY WEATHERED ROCK
45.00		HIGHLY WEATHERED ROCK

BH-32-IN-54/29-13

DEPTH (m)	'N' VALUE	
0.00		
0.25	4	
1.00	6	BROWNISH SILTY SAND (SM)
2.00	9	
3.00	8	GREYISH BROWN SILTY SAND (SP-SM)
4.00	10	BROWNISH SAND (SP)
5.00	12	GREYISH BROWN SILTY SAND (SP-SM)
6.00	18	BROWNISH GREY CLAYEY SAND (SC)
7.50	20	
9.00	25	GREYISH BROWN SANDY CLAY WITH CALCAREOUS DEPOSITS (CI)
10.50	39	
12.00	43	GREYISH BROWN CLAYEY SAND WITH CALCAREOUS DEPOSITS (SC)
13.50	>100	BROWNISH, COMPLETELY WEATHERED, DISINTEGRATED SANDSTONE FRAGMENTS - INTERMEDIATE GEOMATERIAL
		HIGHLY WEATHERED ROCK
45.00		HIGHLY WEATHERED ROCK

BH-33-IN-54/29-14

DEPTH (m)	'N' VALUE	
0.00		
0.25	30	BROWNISH SILTY SAND (SP-SM)
1.00	32	
2.00	35	BROWNISH SILTY SAND (SM)
3.00	27	GREYISH BROWN CLAYEY SAND (SC)
4.00	28	GREYISH BROWN SANDY CLAY (CI)
5.00	30	BROWNISH GREY CLAYEY SAND (SC)
6.00	33	GREYISH BROWN SANDY CLAY (CI)
7.50	32	BROWNISH GREY CLAYEY SAND WITH CALCAREOUS DEPOSITS (SC)
9.00	29	
10.50	30	GREYISH BROWN CLAYEY SAND (SC)
12.00	34	
13.50	32	GREYISH BROWN SILTY SAND (SP-SM)
15.00	>100	BROWNISH, COMPLETELY WEATHERED, DISINTEGRATED SANDSTONE FRAGMENTS - INTERMEDIATE GEOMATERIA
		HIGHLY WEATHERED ROCK
45.00		HIGHLY WEATHERED ROCK

BH-34-IN-54/29-15

DEPTH (m)	'N' VALUE	
0.00		
0.25	6	
1.00	9	BROWNISH CLAYEY SAND (SC)
2.00	10	
3.00	13	GREYISH BROWN SILTY SAND (SM)
4.00	14	
5.00	20	
6.00	19	
7.50	25	BROWNISH SILTY SAND (SP-SM)
9.00	30	GREYISH BROWN SANDY CLAY (CI)
10.50	31	GREYISH BROWN CLAYEY SAND (SC)
12.00	33	
13.50	>100	GREYISH BROWN CLAYEY SAND WITH SANDSTONE FRAGMENTS
15.00	>100	GREYISH BROWN CLAYEY SAND WITH SANDSTONE FRAGMENTS
		HIGHLY WEATHERED ROCK
45.00		HIGHLY WEATHERED ROCK

BH-35-IN-54/29-16

DEPTH (m)	'N' VALUE	
0.00		
0.25	4	BROWNISH SANDY CLAY (CI)
1.00	7	BROWNISH SILTY SAND (SM)
2.00	13	BROWNISH SILTY SAND (SP-SM)
3.00	13	
4.00	15	BROWNISH SILTY SAND (SM)
5.00	13	
6.00	7	GREYISH SILTY CLAY (CI)
7.50	20	GREYISH BROWN CLAYEY SAND (SC)
9.00	22	
10.50	30	
12.00	>100	HIGHLY WEATHERED ROCK
45.00		HIGHLY WEATHERED ROCK

BH-36-INL-54/29-01

DEPTH (m)	'N' VALUE	
0.00		
0.25	6	ROWNISH CLAYEY SAND (SC)
1.00	9	BROWNISH SILTY SAND (SM)
2.00	14	BROWNISH SILTY SAND (SP-SM)
3.00	17	GREYISH BROWN SILTY SAND (SM)
4.00	22	BROWNISH SILTY SAND (SP)
5.00	18	GREYISH SILTY CLAY (CH)
6.00	18	GREYISH CLAYEY SAND (SC)
7.50	25	
9.00	32	GREYISH BROWN CLAYEY SAND WITH CALCAREOUS DEPOSITS (SC)
10.50	30	GREYISH BROWN SANDY CLAY WITH CALCAREOUS DEPOSITS (CI)
12.00	42	GREYISH BROWN CLAYEY SAND (SC)
13.50	50	GREYISH BROWN CLAYEY SAND WITH CALCAREOUS DEPOSITS (SC)
15.00	>100	HIGHLY WEATHERED ROCK
45.00		HIGHLY WEATHERED ROCK

BH-37-INL-54/29-02

DEPTH (m)	'N' VALUE	
0.00		
0.25	6	BROWNISH CLAYEY SAND (SC)
1.00	15	
2.00	14	BROWNISH SILTY SAND (SM)
3.00	18	BROWNISH SILTY SAND (SP-SM)
4.00	22	
5.00	27	BROWNISH SILTY SAND (SM)
6.00	14	BROWNISH GREY SANDY CLAY (CI)
7.50	37	BROWNISH GREY CLAYEY SAND (SC)
9.00	37	
10.50	43	
12.00	56	
13.50	70	
15.00	>100	GREYISH BROWN SITLY SAND (SM)
		HIGHLY WEATHERED ROCK
45.00		HIGHLY WEATHERED ROCK

BH-38-INL-54/29-03

DEPTH (m)	'N' VALUE	
0.00		
0.25	5	BROWNISH SANDY CLAY (CL)
1.00	10	
2.00	14	BROWNISH SILTY SAND (SP-SM)
3.00	17	
4.00	20	GREYISH CLAYEY SAND (SC)
4.50		
5.00	12	BROWNISH GREY SANDY CLAY (CI)
6.00	10	
7.50	18	
9.00	31	BROWNISH GREY CLAYEY SAND (SC)
10.50	41	
12.00	>100	BROWNISH SILTY SAND WITH SANDSTONE FRAGMENTS
		HIGHLY WEATHERED ROCK
45.00		HIGHLY WEATHERED ROCK

BH-39-INL-54/29-04

DEPTH (m)	'N' VALUE	
0.00		
0.25	8	BROWNISH CLAYEY SAND (SC)
1.00	14	GREYISH BROWN SANDY CLAY (CL)
2.00	17	BROWNISH CLAYEY SAND (SC)
3.00	20	
4.00	22	BROWNISH SILTY SAND (SP-SM)
5.00	23	
6.00	10	GREYISH BLACK SILTY CLAY (CH)
7.50	15	
9.00	27	BROWNISH GREY CLAYEY SAND (SC)
10.50	33	GREYISH BROWN CLAYEY SAND WITH CALCAREOUS DEPOSITS (SC)
12.00	40	BROWNISH GREY SANDY CLAY (CI)
12.00	>100	HIGHLY WEATHERED ROCK
45.00		HIGHLY WEATHERED ROCK

BH-40-INL-54/29-05

DEPTH (m)	'N' VALUE	
0.00		
0.25	9	BROWNISH SILTY SAND (SM)
1.00	16	BROWNISH CLAYEY SAND (SC)
2.00	10	BROWNISH SILTY SAND (SP-SM)
3.00	12	BROWNISH SILTY SAND (SM)
4.00	14	BROWNISH CLAYEY SAND (SC)
5.00	17	BROWNISH SILTY SAND (SM)
6.00	23	GREYISH BROWN CLAYEY SAND (SC-CI)
7.50	24	GREYISH SILTY CLAY (CH)
9.00	26	
10.50	33	
12.00	>100	GREYISH BROWN CLAYEY SAND (SC)
		HIGHLY WEATHERED ROCK
45.00		HIGHLY WEATHERED ROCK

BH-41-INL-54/29-06

DEPTH (m)	'N' VALUE	
0.00		
0.25	4	BROWNISH .CLAYEY SAND (SC)
1.00	10	BROWNISH SILTY SAND (SM)
2.00	9	BROWNISH SILTY SAND (SP)
3.00	15	BROWNISH SILTY SAND (SM)
4.00	16	GREYISH SANDY CLAY (CI)
5.00	12	GREYISH BROWN CLAYEY SAND (SC)
6.00	22	BROWNISH SANDY CLAY (CI)
7.50	24	GREYISH BROWN CLAYEY SAND (SC)
9.00	21	GREYISH BROWN CLAYEY SAND WITH CALCAREOUS DEPOSITS (SC)
10.50	36	GREYISH BROWN SANDY CLAY WITH SANDSTONE FRAGMENTS
12.00	23	HIGHLY WEATHERED ROCK
13.50	>100	
		HIGHLY WEATHERED ROCK
45.00		

BH-42-INL-54/29-07

LEGEND:

DF : DEPTH OF FOUNDATION FROM OGL
DGI : DEPTH OF PROPOSED GROUND IMPROVEMENT BELOW FOUNDATION

THIS DRAWING SHALL BE READ IN CONJUNCTION WITH DRAWING NO. O24087-C-RP-MB-GA-8330 (SHEET 1 OF 10)

FOR APPROVAL

REV	DATE	DESCRIPTION	DESIGNED	DRAWN	CHECKED	APPROVED
RB	18.09.25	REVISED AS PER IIT COMMENTS	SSR	SR	ARS	NKC
RA	14.08.25	FOR APPROVAL	SSR	SR	ARS	NKC

CLIENT : TNRIDC
TAMILNADU ROAD INFRASTRUCTURE DEVELOPMENT CORPORATION

AUTHORITY'S ENGINEER : THEME ENGINEERING SERVICE PVT. LTD.,

PROOF CONSULTANT : ASIA INFRASTRUCTURE ADVISORY SERVICES PRIVATE LIMITED

SAFETY CONSULTANT : ALMONDZ GLOBAL INFRA - CONSULTANT LIMITED
(A wholly owned Subsidiary of AGSL)

PROJECT : FORMATION OF NEW SIX LANE ROAD FROM THIRUVALLUR BYPASS (DESIGN CHAINAGE: CH 47+800) TO VENGATHUR (DESIGN CHAINAGE: CH 58+200) WITH PAVED SHOULDERS AND TWO LANE SERVICE ROAD ON BOTH SIDES IN SECTION-3 OF CHENNAI PERIPHERAL RING ROAD PROJECT UNDER PACKAGE-3 ON ENGINEERING, PROCUREMENT AND CONSTRUCTION (EPC) MODE INCLUDING MAINTENANCE FOR 7 YEARS.

CONTRACTOR : L&T Construction, Transportation Infrastructure

DESIGN CONSULTANT : L&T Construction, Transportation Infrastructure, EDRC

AUTHORITY'S ENGINEER | PROOF CONSULTANT | DESIGN DIRECTOR

JOB No. : O24087-C-RP

DESIGNED	SSR	
DRAWN	SR	
CHECKED	ARS	
APPROVED	NKC	
DATE	18.09.2025	SCALE AS SHOWN

TITLE : INTERCHANGE AT CH:54+281
GENERAL ARRANGEMENT OF INTERCHANGE BORE LOG DETAILS

REV: RB
SIZE: A2

DRAWING NO : O 2 4 0 8 7 - C - R P - M B - G A - 8 3 3 0
SHEET: 08 OF 10

Cad File No: D:\CPRR-2\STRUCTURES\INTERCHANGE_MJB\ O24087-C-RP-MB-GA-8330-RC_Interchange at Ch-54+281.dwg

Plot Date: 17 October, 2025 - 5:14 PM

This drawing is the property of TNRIDC and L&T Construction,Transportation Infrastructure and must not be passed on to any person or body not authorised by us to receive it nor be copied or otherwise made use either in full or in part by suchperson or body without our prior permission in writing.

DEPTH (m)	'N' VALUE	
0.00		
0.25	8	BROWNISH CLAYEY SAND (SC)
1.00	12	BROWNISH SILTY SAND (SM)
2.00	13	BROWNISH SILTY SAND (SP-SM)
3.00	16	
4.00	17	BROWNISH SILTY SAND (SM)
5.00	19	BLACKISH SILTY CLAY (CH)
6.00	10	
7.50	23	BROWNISH GREY CLAYEY SAND (SC)
9.00	29	
10.50	25	GREYISH BROWN SANDY CLAY (CL)
12.00	>100	GREYISH BROWN CLAYEY SAND WITH SANDSTONE FRAGMENTS
		HIGHLY WEATHERED ROCK
45.00		HIGHLY WEATHERED ROCK

BH-43-INL-54/29-08

DEPTH (m)	'N' VALUE	
0.00		
0.25	8	BROWNISH CLAYEY SAND (SC)
1.00	11	BROWNISH SILTY SAND (SM)
2.00	12	
3.00	12	BROWNISH SILTY SAND (SP - SM)
4.00	19	
5.00	20	
6.00	15	GREYISH BROWN CLAYEY SAND (SC)
7.50	27	GREYISH BROWN SANDY CLAY (CI)
9.00	36	GREYISH BROWN CLAYEY SAND (SC)
10.50	39	
12.00	>100	GREYISH BROWN, COMPLETELY WEATHERED, DISINTEGRATED AND DECOMPOSED SANDSTONE FRAGMENTS - INTERMEDIATE GEOMATERIAL
		HIGHLY WEATHERED ROCK
45.00		HIGHLY WEATHERED ROCK

BH-44-IN-54/29-09

DEPTH (m)	'N' VALUE	
0.00		
0.25	4	BROWNISH CLAYEY SAND (SC)
1.00	7	BROWNISH SILTY SAND (SM)
2.00	10	
3.00	11	BROWNISH SILTY SAND (SP - SM)
4.00	15	
5.00	17	
6.00	22	BLACKISH CLAYEY SAND (SC)
7.50	33	GREYISH BROWN CLAYEY SAND (SC)
9.00	37	BROWNISH GREY CLAYEY SAND WITH CALCAREOUS DEPOSITS (SC)
10.50	>100	
		HIGHLY WEATHERED ROCK
45.00		HIGHLY WEATHERED ROCK

BH-45-IN-54/29-10

DEPTH (m)	'N' VALUE	
0.00		
	4	
	5	BROWNISH SILTY SAND (SM)
2.00	14	
3.00	10	BROWNISH SILTY SAND (SP-SM)
4.00	15	
5.00	18	BROWNISH SILTY SAND (SM)
6.00	19	BROWNISH GREY SANDY CLAY (CL)
7.50	28	BROWNISH GREY CLAYEY SAND (SC)
9.00	26	GREYISH BROWN SANDY CLAY WITH CALCAREOUS MATERIALS (CI)
10.50	32	GREYISH BROWN CLAYEY SAND WITH CALCAREOUS MATERIALS (SC)
12.00	>100	GREYISH BROWN SANDY CLAY WITH SANDSTONE FRAGMENTS
		HIGHLY WEATHERED ROCK
45.00		HIGHLY WEATHERED ROCK

BH-46-INL-54/29-11

DEPTH (m)	'N' VALUE	
0.00		
0.25	7	BROWNISH CLAYEY SAND (SC)
1.00	9	BROWNISH SANDY CLAY (CI)
2.00	10	BROWNISH SILTY SAND (SM)
3.00	11	BROWNISH SILTY SAND (SP - SM)
4.00	15	
5.00	21	BROWNISH GREY CLAYEY SAND (SC)
6.00	35	
7.50	38	GREYISH BROWN SANDY CLAY (CI)
9.00	45	GREYISH BROWN CLAYEY SAND WITH CALCAREOUS DEPOSITS (SC)
10.50	46	
12.00	>100	GREYISH BROWN CLAYEY SAND WITH SANDSTONE FRAGMENTS
		HIGHLY WEATHERED ROCK
45.00		HIGHLY WEATHERED ROCK

BH-47-IN-54/29-12

DEPTH (m)	'N' VALUE	
0.00		
0.25	6	
1.00	7	BROWNISH SILTY SAND (SM)
2.00	10	BROWNISH SILTY SAND (SP - SM)
3.00	12	BROWNISH SAND (SP)
4.00	13	BROWNISH SILTY SAND (SP - SM)
5.00	16	BROWNISH GREY CLAYEY SAND (SC)
6.00	19	
7.50	31	GREYISH BROWN CLAYEY SAND WITH CALCAREOUS DEPOSITS (SC)
9.00	25	
10.50	>100	GREYISH BROWN CLAYEY SAND WITH SANDSTONE FRAGMENTS
		HIGHLY WEATHERED ROCK
45.00		HIGHLY WEATHERED ROCK

BH-48-IN-54/29-13

DEPTH (m)	'N' VALUE	
0.00		
0.25	7	GREYISH BROWN CLAYEY SAND (SC)
1.00	10	BROWNISH SILTY SAND (SP-SM)
2.00	14	
3.00	16	BROWNISH SAND (SP)
4.00	21	
5.00	24	BROWNISH SILTY SAND (SP-SM)
6.00	18	GREYISH BROWN CLAYEY SAND WITH CALCAREOUS MATERIALS (SC)
7.50	20	BROWNISH GREY CLAYEY SAND (SC)
9.00	24	BROWNISH GREY SANDY CLAY (CI)
10.50	>100	GREYISH BROWN CLAYEY SAND WITH CALCAREOUS MATERIALS (SC)
12.00	>100	BROWNISH CLAYEY SAND WITH SANDSTONE FRAGMENTS
		HIGHLY WEATHERED ROCK
45.00		HIGHLY WEATHERED ROCK

BH-49-IN-54/29-14

DEPTH (m)	'N' VALUE	
0.00		
0.25	6	GREYISH CLAYEY SAND (SC)
1.00	10	BROWNISH SILTY SAND (SP-SM)
2.00	11	BROWNISH SAND (SP)
3.00	14	BROWNISH SILTY SAND (SP-SM)
4.00	18	BROWNISH SILTY SAND (SM)
5.00	18	GREYISH BROWN CLAYEY SAND (SC)
6.00	22	GREYISH BROWN SANDY CLAY (CI)
7.50	23	GREYISH BROWN CLAYEY SAND WITH CALCAREOUS MATERIALS (SC)
9.00	36	
10.50	43	
12.00	>100	GREYISH BROWN CLAYEY SAND WITH SANDSTONE FRAGMENTS
13.50	>100	
		HIGHLY WEATHERED ROCK
45.00		HIGHLY WEATHERED ROCK

BH-50-IN-54/29-15

DEPTH (m)	'N' VALUE	
0.00		
0.25	4	BROWNISH CLAYEY SAND (SC)
1.00	7	BROWNISH SILTY SAND (SM)
2.00	8	
3.00	15	BROWNISH SILTY SAND (SP-SM)
4.00	16	
5.00	17	GREYISH BLACK SILTY CLAY (CH)
6.00	15	GREYISH BROWN CLAYEY SAND (SC)
7.50	20	GREYISH BROWN CLAYEY SAND WITH CALCAREOUS MATERIALS (SC)
9.00	26	GREYISH BROWN CLAYEY SAND WITH CALCAREOUS MATERIALS (SC-CI)
10.50	26	
12.00	30	GREYISH BROWN CLAYEY SAND WITH CALCAREOUS MATERIALS (SC)
13.50	31	
15.00	>100	HIGHLY WEATHERED ROCK
45.00		HIGHLY WEATHERED ROCK

BH-51-IN-54/29-16

DEPTH (m)	'N' VALUE	
0.00		
0.25	5	BROWNISH SANDY CLAY (CL)
1.00	6	
2.00	7	BROWNISH GREY SILTY SAND (SM)
3.00	9	
4.00	13	BROWNISH GREY CLAYEY SAND (SC)
5.00	16	
6.00	19	BROWNISH GREY CLAYEY SAND (SC - CL)
7.50	20	BROWNISH GREY CLAYEY SAND (SC)
9.00	23	
10.50	25	
12.00	24	
13.50	>100	BROWNISH SANDY CLAY WITH SANDSTONE FRAGMENTS
		HIGHLY WEATHERED ROCK
45.00		HIGHLY WEATHERED ROCK

BH-52-INL-54/29-17

DEPTH (m)	'N' VALUE	
0.00		
0.25	9	BROWNISH SILTY SAND (SM)
1.00	12	BROWNISH SAND (SP)
2.00	13	
3.00	15	BROWNISH GREY CLAYEY SAND (SC)
4.00	17	
5.00	18	BROWNISH GREY CLAYEY SAND (SC-CL)
6.00	21	BROWNISH GREY CLAYEY SAND (SC)
7.50	25	BROWNISH GREY CLAYEY SAND WITH CALCAREOUS DEPOSITS(SC)
9.00	23	GREYISH BROWN SANDY CLAY (CI)
10.50	27	GREYISH BROWN CLAYEY SAND (SC)
12.00	>100	GREYISH BROWN CLAYEY SAND WITH SANDSTONE FRAGMENTS
		HIGHLY WEATHERED ROCK
45.00		HIGHLY WEATHERED ROCK

BH-53-INL-54/29-18

DEPTH (m)	'N' VALUE	
0.00		
0.25	7	
1.00	8	BROWNISH SILTY SAND (SM)
2.00	12	GREYISH SILTY SAND (SP-SM)
3.00	14	
4.00	16	GREYISH SILTY CLAY (CH)
5.00	21	
6.00	22	BROWNISH GREY SANDY CLAY (CI)
7.50	19	
9.00	23	BROWNISH GREY CLAYEY SAND (SC)
10.50	29	
12.00	31	GREYISH BROWN CLAYEY SAND WITH CALCAREOUS DEPOSITS (SC)
13.50	35	GREYISH BROWN SANDY CLAY WITH CALCAREOUS DEPOSITS (CI)
15.00	38	BROWNISH CLAYEY SAND WITH CALCAREOUS DEPOSITS (SC)
16.50	>100	BROWNISH SANDY CLAY WITH SANDSTONE FRAGMENTS
		HIGHLY WEATHERED ROCK
45.00		

BH-54-INL-54/29-19

LEGEND:

DF : DEPTH OF FOUNDATION FROM OGL
DGI : DEPTH OF PROPOSED GROUND IMPROVEMENT BELOW FOUNDATION

THIS DRAWING SHALL BE READ IN CONJUNCTION WITH DRAWING NO. O24087-C-RP-MB-GA-8330 (SHEET 1 OF 10)

FOR APPROVAL

REV	DATE	DESCRIPTION	DESIGNED	DRAWN	CHECKED	APPROVED
RB	18.09.25	REVISED AS PER IIT COMMENTS	SSR	SR	ARS	NKC
RA	14.08.25	FOR APPROVAL	SSR	SR	ARS	NKC

CLIENT : TNRIDC
TAMILNADU ROAD INFRASTRUCTURE DEVELOPMENT CORPORATION

AUTHORITY'S ENGINEER : THEME ENGINEERING SERVICE PVT. LTD.,

PROOF CONSULTANT : ASIA INFRASTRUCTURE ADVISORY SERVICES PRIVATE LIMITED

SAFETY CONSULTANT : ALMONDZ GLOBAL INFRA - CONSULTANT LIMITED
(A wholly owned Subsidiary of AGSL)

PROJECT : FORMATION OF NEW SIX LANE ROAD FROM THIRUVALLUR BYPASS (DESIGN CHAINAGE: CH 47+800) TO VENGATHUR (DESIGN CHAINAGE: CH 58+200) WITH PAVED SHOULDERS AND TWO LANE SERVICE ROAD ON BOTH SIDES IN SECTION-3 OF CHENNAI PERIPHERAL RING ROAD PROJECT UNDER PACKAGE-3 ON ENGINEERING, PROCUREMENT AND CONSTRUCTION (EPC) MODE INCLUDING MAINTENANCE FOR 7 YEARS.

CONTRACTOR : L&T Construction, Transportation Infrastructure

DESIGN CONSULTANT : L&T Construction, Transportation Infrastructure, EDRC

AUTHORITY'S ENGINEER | PROOF CONSULTANT | DESIGN DIRECTOR

JOB No. : O24087-C-RP

DESIGNED	SSR	
DRAWN	SR	
CHECKED	ARS	
APPROVED	NKC	
DATE	14.08.2025	SCALE AS SHOWN

TITLE : INTERCHANGE AT CH:54+281
GENERAL ARRANGEMENT OF INTERCHANGE BORE LOG DETAILS

REV: RB
SIZE: A2

DRAWING NO : O 2 4 0 8 7 - C - R P - M B - G A - 8 3 3 0
SHEET: 09 OF 10

Cad File No: D:\CPRR-2\STRUCTURES\INTERCHANGE_MJB\ O24087-C-RP-MB-GA-8330-RC_Interchange at Ch-54+281.dwg

Plot Date: 17 October, 2025 - 5:14 PM

This drawing is the property of TNRIDC and L&T Construction,Transportation Infrastructure and must not be passed on to any person or body not authorised by us to receive it nor be copied or otherwise made use either in full or in part by suchperson or body without our prior permission in writing.

DEPTH (m)	'N' VALUE	
0.00		
0.25	5	GREYISH BROWN CLAYEY SAND (SC)
1.00	8	
2.00	11	BROWNISH SILTY SAND (SM)
3.00	20	BROWNISH GREY SILTY SAND (SP - SM)
4.00	22	
5.00	25	GREYISH SAND (SP)
6.00	18	GREYISH SILTY CLAY (CH)
7.50	27	GREYISH SANDY CLAY (CI)
9.00	33	GREYISH BROWN CLAYEY SAND WITH CALCAREOUS DEPOSITS (SC)
10.50	36	GREYISH BROWN SANDY CLAY WITH CALCAREOUS DEPOSITS (CI)
12.00	37	
13.50	39	
15.00	34	GREYISH BROWN SILTY CLAY WITH CALCAREOUS DEPOSITS (CH)
16.50	40	BROWNISH GREY CLAYEY SAND WITH CALCAREOUS DEPOSITS (SC)
18.00	>100	BROWNISH CLAYEY SAND WITH SANDSTONE FRAGMENT
		HIGHLY WEATHERED ROCK
45.00		HIGHLY WEATHERED ROCK

BH-55-INL-54/29-20

DEPTH (m)	'N' VALUE	
0.00		
0.25	6	GREYISH BROWN CLAYEY SAND (SC)
1.00	9	BROWNISH SILTY SAND (SM)
2.00	15	
3.00	15	GREYISH BROWN SAND (SP)
4.00	17	GREYISH BROWN SILTY SAND (SP - SM)
5.00	23	GREYISH BROWN SAND (SP)
6.00	15	BLACKISH SILTY CLAY (CH)
7.50	26	BROWNISH GREY SANDY CLAY (CI)
9.00	30	BROWNISH GREY CLAYEY SAND WITH CALCAREOUS DEPOSITS (SC)
10.50	35	
12.00	38	GREYISH BROWN SANDY CLAY (CI)
13.50	39	
15.00	40	BROWNISH CLAYEY SAND WITH CALCAREOUS DEPOSITS (SC)
16.50	>100	BROWNISH GREY CLAYEY SAND WITH SANDSTONE FRAGMENTS
		HIGHLY WEATHERED ROCK
45.00		HIGHLY WEATHERED ROCK

BH-56-INL-54/29-21

DEPTH (m)	'N' VALUE	
0.00		
	7	BROWNISH SILTY SAND (SM)
	8	
2.00	8	
	11	GREYISH BROWN SILTY SAND (SP - SM)
4.00	15	
5.00	17	GREYISH SANDY CLAY (CI)
	16	BROWNISH GREY CLAYEY SAND (SC)
	15	
9.00	21	
10.50	26	BROWNISH GREY CLAYEY SAND WITH CALCAREOUS DEPOSITS (SC)
12.00	>100	GREYISH CLAYEY SAND WITH SANDSTONE FRAGMENTS
		HIGHLY WEATHERED ROCK
45.00		HIGHLY WEATHERED ROCK

BH-57-INL-54/29-22

DEPTH (m)	'N' VALUE	
0.00		
1.00	9	BROWNISH SAND (SP)
2.00	10	BROWNISH SILTY SAND (SP-SM)
3.00	12	
4.00	16	
5.00	17	BROWNISH SAND (SP)
6.00	14	GREYISH CLAYEY SAND (SC)
7.50	15	
9.00	21	
10.50	28	BROWNISH GREY SANDY CLAY (CI)
12.00	30	GREYISH CLAYEY SAND (SC)
13.50	44	
15.00	>100	BROWNISH GREY SILTY SAND WITH SANDSTONE FRAGMENTS
		HIGHLY WEATHERED ROCK
45.00		HIGHLY WEATHERED ROCK

BH-58 (IN-54/29-24)

DEPTH (m)	'N' VALUE	
0.00		
1.00	5	BROWNISH SILTY SAND (SM)
2.00	7	
3.00	16	WELL GRADED-SILTY SAND (SW-SM)
4.00	11	
5.00	17	
6.00	10	BROWNISH POORLY GRADED SAND (SP)
7.50	10	
9.00	10	BROWN CLAYEY SAND (SC)
10.50	16	BROWNISH GREY SAND CLAY (CI)
12.00	29	GREYISH SILTY CLAY (CH)
13.50	>100	BROWN CLAYEY SAND (SC)
15.00	66	BROWNISH SILTY SAND (SM)
	>100	
19.50	>100	BROWN CLAYEY SAND (SC)
22.50		BROWNISH SILTY SAND (SM)
27.00	89	
	>100	BROWN CLAYEY SAND (SC)
36.00	63	GREYISH SILTY CLAY (CH)
	>100	
45.00		HIGHLY WEATHERED ROCK

BH-59 (IN-54/29-24)

DEPTH (m)	'N' VALUE	
0.00		
0.25	11	BROWNISH GREY CLAYEY SAND (SC)
1.00	13	
2.00	15	BROWNISH SILTY SAND (SP - SM)
3.00	18	BROWNISH CLAYEY SAND (SC)
4.00	19	BROWNISH SILTY SAND (SP - SM)
5.00	20	
6.00	25	BROWNISH SILTY SAND (SM)
7.50	28	GREYISH BROWN CLAYEY SAND (SC)
9.00	31	GREYISH BROWN SANDY CLAY (CI)
10.50	33	
12.00	35	BROWNISH GREY CLAYEY SAND WITH CALCAREOUS DEPOSITS (SC)
13.50	40	
15.00	>100	BROWNISH SILTY SAND WITH SANDSTONE FRAGMENTS
		HIGHLY WEATHERED ROCK
45.00		HIGHLY WEATHERED ROCK

BH-60-INL-54/29-25

DEPTH (m)	'N' VALUE	
0.00		
1.00		FILLED UP SOIL
2.00		
3.00	10	BROWNISH SAND (SP)
4.00	11	BROWNISH SILTY SAND (SP-SM)
5.00	21	BROWNISH SILTY SAND (SM)
6.00	24	
7.50	27	BROWNISH GREY CLAYEY SAND (SC)
9.00	30	
10.50	24	
12.00	29	BROWNISH GREY SANDY CLAY (CI)
13.50	35	GREYISH BROWN CLAYEY SAND WITH CALCAREOUS MATERIALS (SC)
15.00	>100	BROWNISH CLAYEY SAND WITH SANDSTONE FRAGMENTS
		HIGHLY WEATHERED ROCK
45.00		HIGHLY WEATHERED ROCK

BH-61 (IN-54/29-27)

DEPTH (m)	'N' VALUE	
0.00		
2.00	6	BROWNISH SILTY SAND (SM)
3.00	13	
4.00	16	WELL GRADED-SILTY SAND (SW-SM)
5.00	11	GREYISH SILTY SAND (SP-SM)
6.00	12	
7.50	16	WELL GRADED-SILTY SAND (SW-SM)
9.00	15	
12.00	27	
13.50	37	BROWN CLAYEY SAND (SC)
15.00	66	
16.50	>100	BROWNISH SILTY SAND (SM)
21.00	89	BROWNISH SILTY SAND (SM)
22.50	>100	BROWN CLAYEY SAND (SC)
		HIGHLY WEATHERED ROCK
45.00		HIGHLY WEATHERED ROCK

BH-62 (IN-54/29-27)

DEPTH (m)	'N' VALUE	
0.00		
0.25	3	BROWNISH CLAYEY SAND (SC)
1.00	7	BROWNISH SILTY SAND (SM)
2.00	9	BROWNISH SILTY SAND (SP - SM)
3.00	11	BROWNISH SAND (SP)
4.00	14	BROWNISH SILTY SAND (SP - SM)
5.00	15	BROWNISH CLAYEY SAND (SC)
6.00	19	GREYISH BROWN SAND (SP)
7.50	22	GREYISH BROWN CLAYEY SAND (SC)
9.00	21	
10.50	26	BROWNISH CLAYEY SAND WITH CALCAREOUS DEPOSITS (SC)
12.00	>100	
13.50	>100	BROWNISH GREY CLAYEY SAND WITH CALCAREOUS DEPOSITS (SC - CI)
15.00	>100	BROWNISH GREY CLAYEY SAND WITH CALCAREOUS DEPOSITS (SC)
		HIGHLY WEATHERED ROCK
45.00		HIGHLY WEATHERED ROCK

BH-63-INL-54/29-28

DEPTH (m)	'N' VALUE	
0.00		
0.25	4	BROWNISH GREY CLAYEY SAND (SC)
1.00	6	BROWNISH SILTY SAND (SM)
2.00	12	
3.00	21	BROWNISH SILTY SAND (SP - SM)
4.00	19	
5.00	24	
6.00	25	GREYISH BROWN CLAYEY SAND (SC)
7.50	29	
9.00	34	GREYISH BROWN CLAYEY SAND WITH CALCAREOUS DEPOSITS (SC)
10.50	41	
12.00	>100	
		HIGHLY WEATHERED ROCK
45.00		HIGHLY WEATHERED ROCK

BH-64-INL-54/29-29

DEPTH (m)	'N' VALUE	
0.00		
0.25	8	BROWNISH CLAYEY SAND (SC)
1.00	12	
2.00	11	BROWNISH SILTY SAND (SP - SM)
3.00	14	BROWNISH SILTY SAND (SM)
4.00	17	BROWNISH SILTY SAND (SP - SM)
5.00	25	GREYISH BROWN SILTY SAND (SM)
6.00	33	BROWNISH GREY CLAYEY SAND WITH CALCAREOUS DEPOSITS (SC - CI)
7.50	39	BROWNISH GREY SANDY CLAY (CI)
9.00	35	BROWNISH GREY CLAYEY SAND (SC)
10.50	37	BROWNISH GREY SANDY CLAY WITH CALCAREOUS DEPOSITS (CI)
12.00	42	GREYISH BROWN CLAYEY SAND WITH SANDSTONE FRAGMENTS
13.50	>100	HIGHLY WEATHERED ROCK
		HIGHLY WEATHERED ROCK
45.00		

BH-65-INL-54/29-30

LEGEND:

DF : DEPTH OF FOUNDATION FROM OGL
DGI : DEPTH OF PROPOSED GROUND IMPROVEMENT BELOW FOUNDATION

THIS DRAWING SHALL BE READ IN CONJUNCTION WITH DRAWING NO. O24087-C-RP-MB-GA-8330 (SHEET 1 OF 10)

FOR APPROVAL

REV	DATE	DESCRIPTION	DESIGNED	DRAWN	CHECKED	APPROVED
RB	18.09.25	REVISED AS PER IIT COMMENTS	SSR	SR	ARS	NKC
RA	14.08.25	FOR APPROVAL	SSR	SR	ARS	NKC

CLIENT : TNRIDC
TAMILNADU ROAD INFRASTRUCTURE DEVELOPMENT CORPORATION

AUTHORITY'S ENGINEER : THEME ENGINEERING SERVICE PVT. LTD.,

PROOF CONSULTANT : ASIA INFRASTRUCTURE ADVISORY SERVICES PRIVATE LIMITED

SAFETY CONSULTANT : ALMONDZ GLOBAL INFRA - CONSULTANT LIMITED (A wholly owned Subsidiary of AGSL)

PROJECT : FORMATION OF NEW SIX LANE ROAD FROM THIRUVALLUR BYPASS (DESIGN CHAINAGE: CH 47+800) TO VENGATHUR (DESIGN CHAINAGE: CH 58+200) WITH PAVED SHOULDERS AND TWO LANE SERVICE ROAD ON BOTH SIDES IN SECTION-3 OF CHENNAI PERIPHERAL RING ROAD PROJECT UNDER PACKAGE-3 ON ENGINEERING, PROCUREMENT AND CONSTRUCTION (EPC) MODE INCLUDING MAINTENANCE FOR 7 YEARS.

CONTRACTOR : L&T Construction, Transportation Infrastructure

DESIGN CONSULTANT : L&T Construction, Transportation Infrastructure, EDRC

AUTHORITY'S ENGINEER | PROOF CONSULTANT | DESIGN DIRECTOR

JOB No. : O24087-C-RP

DESIGNED	SSR	
DRAWN	SR	
CHECKED	ARS	
APPROVED	NKC	
DATE	14.08.2025	
SCALE	AS SHOWN	

TITLE : INTERCHANGE AT CH:54+281
GENERAL ARRANGEMENT OF INTERCHANGE BORE LOG DETAILS

REV: RB
SIZE: A2

DRAWING NO : O 2 4 0 8 7 - C - R P - M B - G A - 8 3 3 0
SHEET: 10 OF 10

Cad File No: D:\CPRR-2\STRUCTURES\INTERCHANGE_MJB\ O24087-C-RP-MB-GA-8330-RC_Interchange at Ch-54+281.dwg

Plot Date: 17 October, 2025 - 5:15 PM