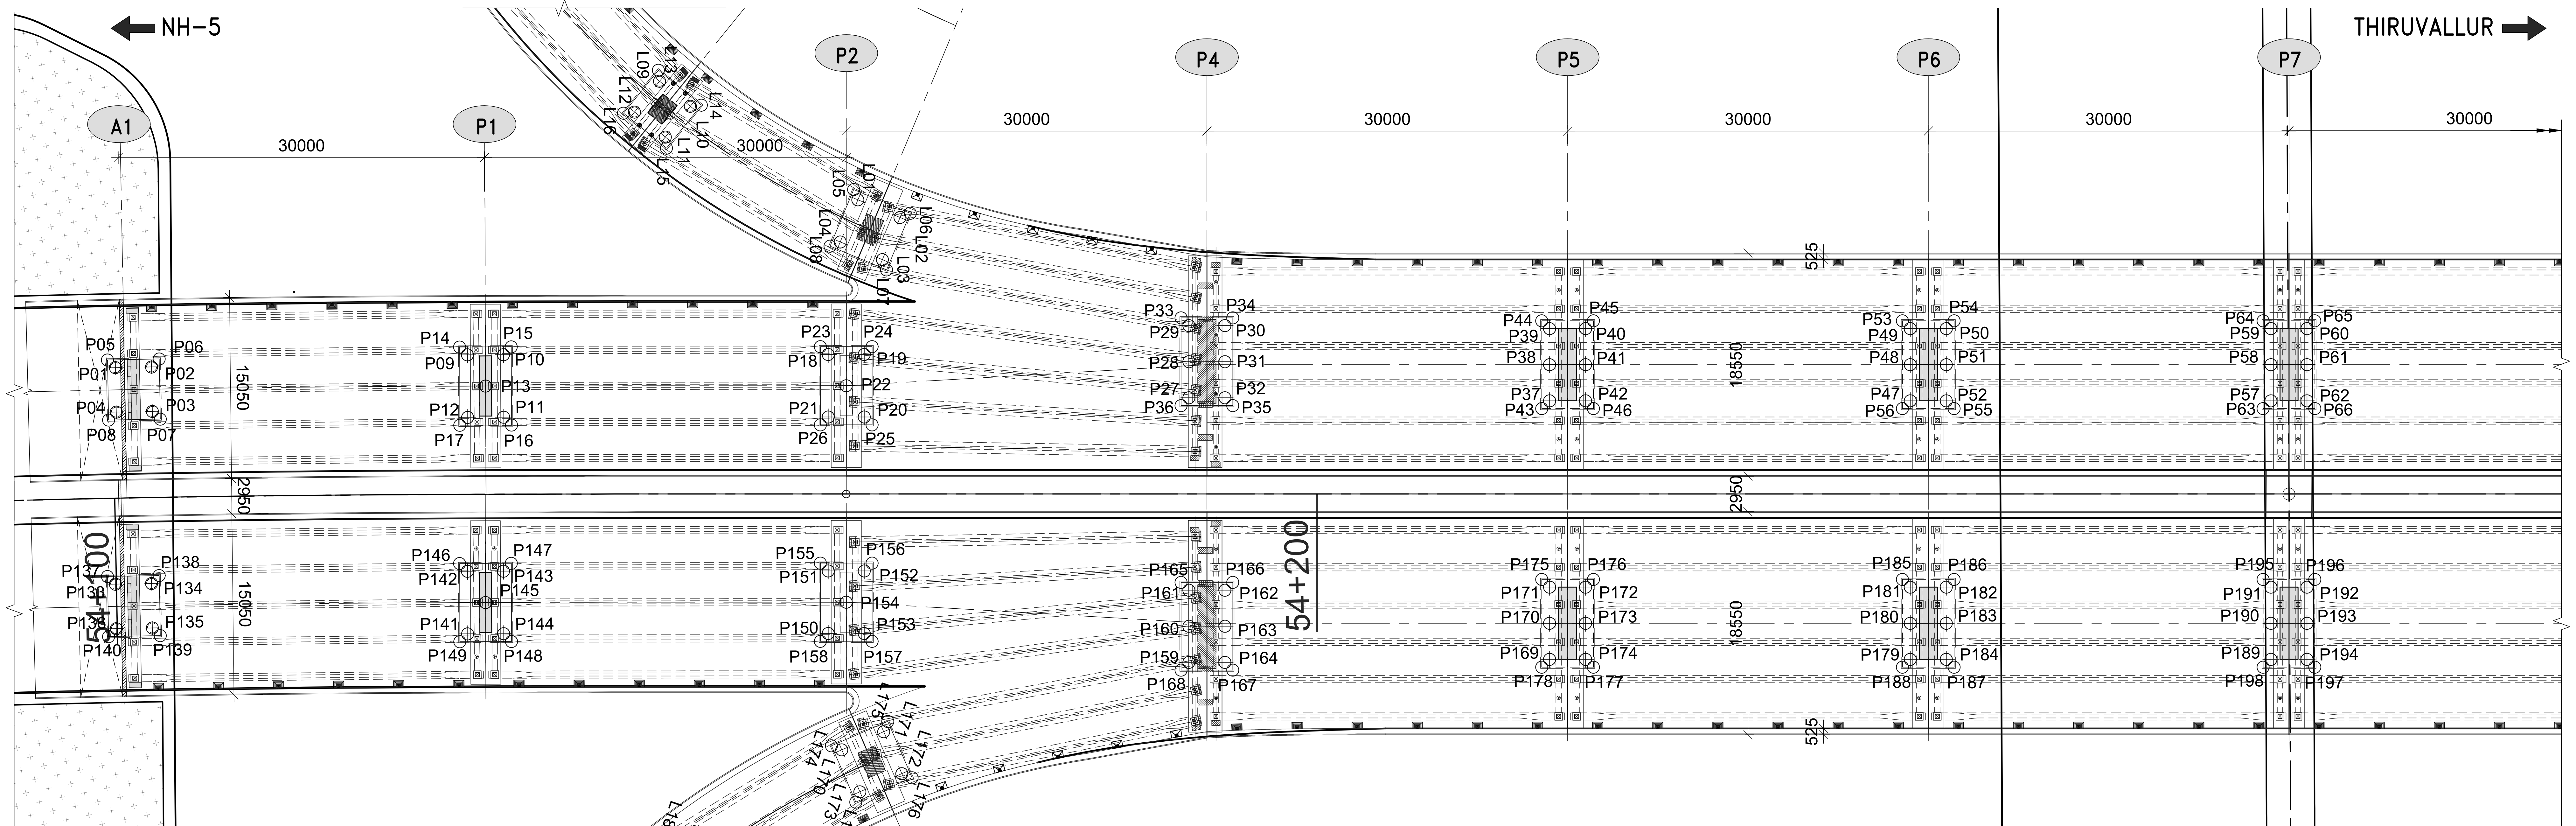

PLAN

LHS CARRIAGE WAY COORDINATES

PIER	POINTS	EASTING (X)	NORTHING (Y)
A1	P01	385999.744	1452420.52
	P02	385999.202	1452417.569
	P03	385995.563	1452418.237
	P04	385996.104	1452421.188
	P05	386000.5	1452421.042
	P06	385999.724	1452416.812
	P07	385994.806	1452417.715
	P08	385995.582	1452421.945
P1	P09	385994.955	1452391.621
	P10	385994.368	1452388.679
	P11	385989.268	1452389.696
	P12	385989.855	1452392.638
	P13	385992.111	1452390.658
	P14	385995.719	1452392.131
	P15	385994.878	1452387.914
	P16	385988.504	1452389.186
	P17	385989.345	1452393.403
P2	P18	385989.006	1452362.207
	P19	385988.408	1452359.267
	P20	385983.312	1452360.303
	P21	385983.91	1452363.243
	P22	385986.159	1452361.255
	P23	385989.772	1452362.714
	P24	385988.915	1452358.501
	P25	385982.546	1452359.796
	P26	385983.402	1452364.009
P4	P27	385979.501	1452333.526
	P28	385982.441	1452332.928
	P29	385985.38	1452332.33
	P30	385984.783	1452329.39
	P31	385981.843	1452329.988
	P32	385978.903	1452330.586
	P33	385986.147	1452332.838
	P34	385985.29	1452328.624
	P35	385978.137	1452330.078
	P36	385978.993	1452334.292

LHS CARRIAGE WAY COORDINATES

PIER	POINTS	EASTING (X)	NORTHING (Y)
P5	P37	385973.279	1452304.177
	P38	385976.219	1452303.579
	P39	385979.159	1452302.981
	P40	385978.561	1452300.042
	P41	385975.621	1452300.639
	P42	385972.681	1452301.237
	P43	385972.771	1452304.943
	P44	385979.925	1452303.489
	P45	385979.068	1452299.275
	P46	385971.915	1452300.729
P6	P47	385967.302	1452274.778
	P48	385970.242	1452274.181
	P49	385973.182	1452273.583
	P50	385972.584	1452270.643
	P51	385969.644	1452271.241
	P52	385966.704	1452271.838
	P53	385973.948	1452274.09
	P54	385973.091	1452269.877
	P55	385965.938	1452271.331
	P56	385966.794	1452275.545
P7	P57	385961.325	1452245.38
	P58	385964.265	1452244.782
	P59	385967.205	1452244.184
	P60	385966.607	1452241.244
	P61	385963.667	1452241.842
	P62	385960.727	1452242.44
	P63	385960.818	1452246.146
	P64	385967.971	1452244.692
	P65	385967.114	1452240.478
	P66	385959.961	1452241.932

RHS CARRIAGE WAY COORDINATES

PIER	POINTS	EASTING (X)	NORTHING (Y)
A1	P133	385982.101	1452424.106
	P134	385981.559	1452421.156
	P135	385977.92	1452421.824
	P136	385978.462	1452424.775
	P137	385982.858	1452424.628
	P138	385982.081	1452420.399
	P139	385977.163	1452421.302
	P140	385977.94	1452425.531
P1	P141	385972.217	1452396.225
	P142	385977.316	1452395.206
	P143	385976.728	1452392.264
	P144	385971.629	1452393.284
	P145	385974.472	1452394.245
	P146	385978.081	1452395.716
	P147	385977.238	1452391.499
	P148	385970.864	1452392.774
	P149	385971.707	1452396.99
P2	P150	385966.271	1452366.829
	P151	385971.366	1452365.793
	P152	385970.769	1452362.853
	P153	385965.673	1452363.889
	P154	385968.52	1452364.841
	P155	385972.133	1452366.301
	P156	385971.276	1452362.087
	P157	385964.906	1452363.382
	P158	385965.763	1452367.596
P4	P159	385957.942	1452337.909
	P160	385960.882	1452337.311
	P161	385963.822	1452336.713
	P162	385963.224	1452333.773
	P163	385960.284	1452334.371
	P164	385957.344	1452334.969
	P165	385964.588	1452337.221
	P166	385963.731	1452333.007
	P167	385956.578	1452334.461
	P168	385957.434	1452338.675

RHS CARRIAGE WAY COORDINATES

PIER	POINTS	EASTING (X)	NORTHING (Y)
P5	P169	385952.21	1452308.46
	P170	385955.15	1452307.863
	P171	385958.09	1452307.265
	P172	385957.492	1452304.325
	P173	385954.552	1452304.923
	P174	385951.612	1452305.52
	P175	385958.856	1452307.772
	P176	385957.999	1452303.559
	P177	385950.846	1452305.013
	P178	385951.702	1452309.227
P6	P179	385946.233	1452279.062
	P180	385949.173	1452278.464
	P181	385952.113	1452277.866
	P182	385951.515	1452274.926
	P183	385948.575	1452275.524
	P184	385945.635	1452276.122
	P185	385952.879	1452278.374
	P186	385952.022	1452274.16
	P187	385944.869	1452275.614
	P188	385945.725	1452279.828
P7	P189	385940.256	1452249.663
	P190	385943.196	1452249.065
	P191	385946.136	1452248.468
	P192	385945.538	1452245.528
	P193	385942.598	1452246.126
	P194	385939.658	1452246.723
	P195	385946.902	1452248.975
	P196	385946.045	1452244.761
	P197	385938.892	1452246.216
	P198	385939.749	1452250.43

REFERENCE DRAWING:-

1. GENERAL ARRANGEMENT DRAWING FOR INTERCHANGE AT CH: 57+542 - O24087-C-RP-MB-GA-8330

NOTES:

1. ALL DIMENSIONS ARE IN MILLIMETERS ,LEVELS AND CHAINAGES ARE IN METERS. UNLESS OTHERWISE MENTIONED.
2. DIMENSIONS ARE NOT TO BE SCALED, ONLY WRITTEN DIMENSIONS SHALL BE FOLLOWED.

THIS DRAWING SHALL BE READ IN CONJUNCTION WITH DRAWING NO. O24087-C-RP-MB-GA-8330

REV	DATE	DESCRIPTION	DESIGNED	DRAWN	CHECKED	APPROVED
RB	22.10.25	REVISED BASED ON SITE CONDITION	SRR	SR	ARS	NKC
RA	20.08.25	FOR APPROVAL	SRR	SRA	ARS	NKC

CLIENT :
TNRIDC
TAMILNADU ROAD INFRASTRUCTURE DEVELOPMENT CORPORATION

AUTHORITY'S ENGINEER :
TES THEME ENGINEERING SERVICE PVT. LTD.,

PROOF CONSULTANT :
ASIA INFRASTRUCTURE ADVISORY SERVICES PRIVATE LIMITED

SAFETY CONSULTANT :
almondz ALMONDZ GLOBAL INFRA - CONSULTANT LIMITED
(A wholly owned Subsidiary of AGSL)

PROJECT :
FORMATION OF NEW SIX LANE ROAD FROM THIRUVALLUR BYPASS (DESIGN CHAINAGE: CH 47+800) TO VENGATHUR (DESIGN CHAINAGE: CH 58+200) WITH PAVED SHOULDERS AND TWO LANE SERVICE ROAD ON BOTH SIDES IN SECTION-3 OF CHENNAI PERIPHERAL RING ROAD PROJECT UNDER PACKAGE-3 ON ENGINEERING, PROCUREMENT AND CONSTRUCTION (EPC) MODE INCLUDING MAINTENANCE FOR 7 YEARS.

CONTRACTOR :
L&T Construction
Transportation Infrastructure

DESIGN CONSULTANT :
L&T Construction
Transportation Infrastructure, EDRC

AUTHORITY'S ENGINEER
PROOF CONSULTANT
ASIA INFRASTRUCTURE ADVISORY SERVICES (P) LTD.
DESIGN DIRECTOR
L&T CONSTRUCTION CHENNAI
DESIGN DIRECTOR

JOB No. : O24087-C-RP

DESIGNED	SRR	
DRAWN	SRA	S Ranjitha
CHECKED	ARS	
APPROVED	NKC	NKC
DATE	SCALE	
20.08.2025		

TITLE : INTERCHANGE AT CH:54+281
FOUNDATION LAYOUT FOR INTERCHANGE - MAIN CARRIAGE WAY

REV: RB
SIZE: A2

DRAWING NO : O24087-C-RP-MB-NU-8390

SHEET: 01 OF 04

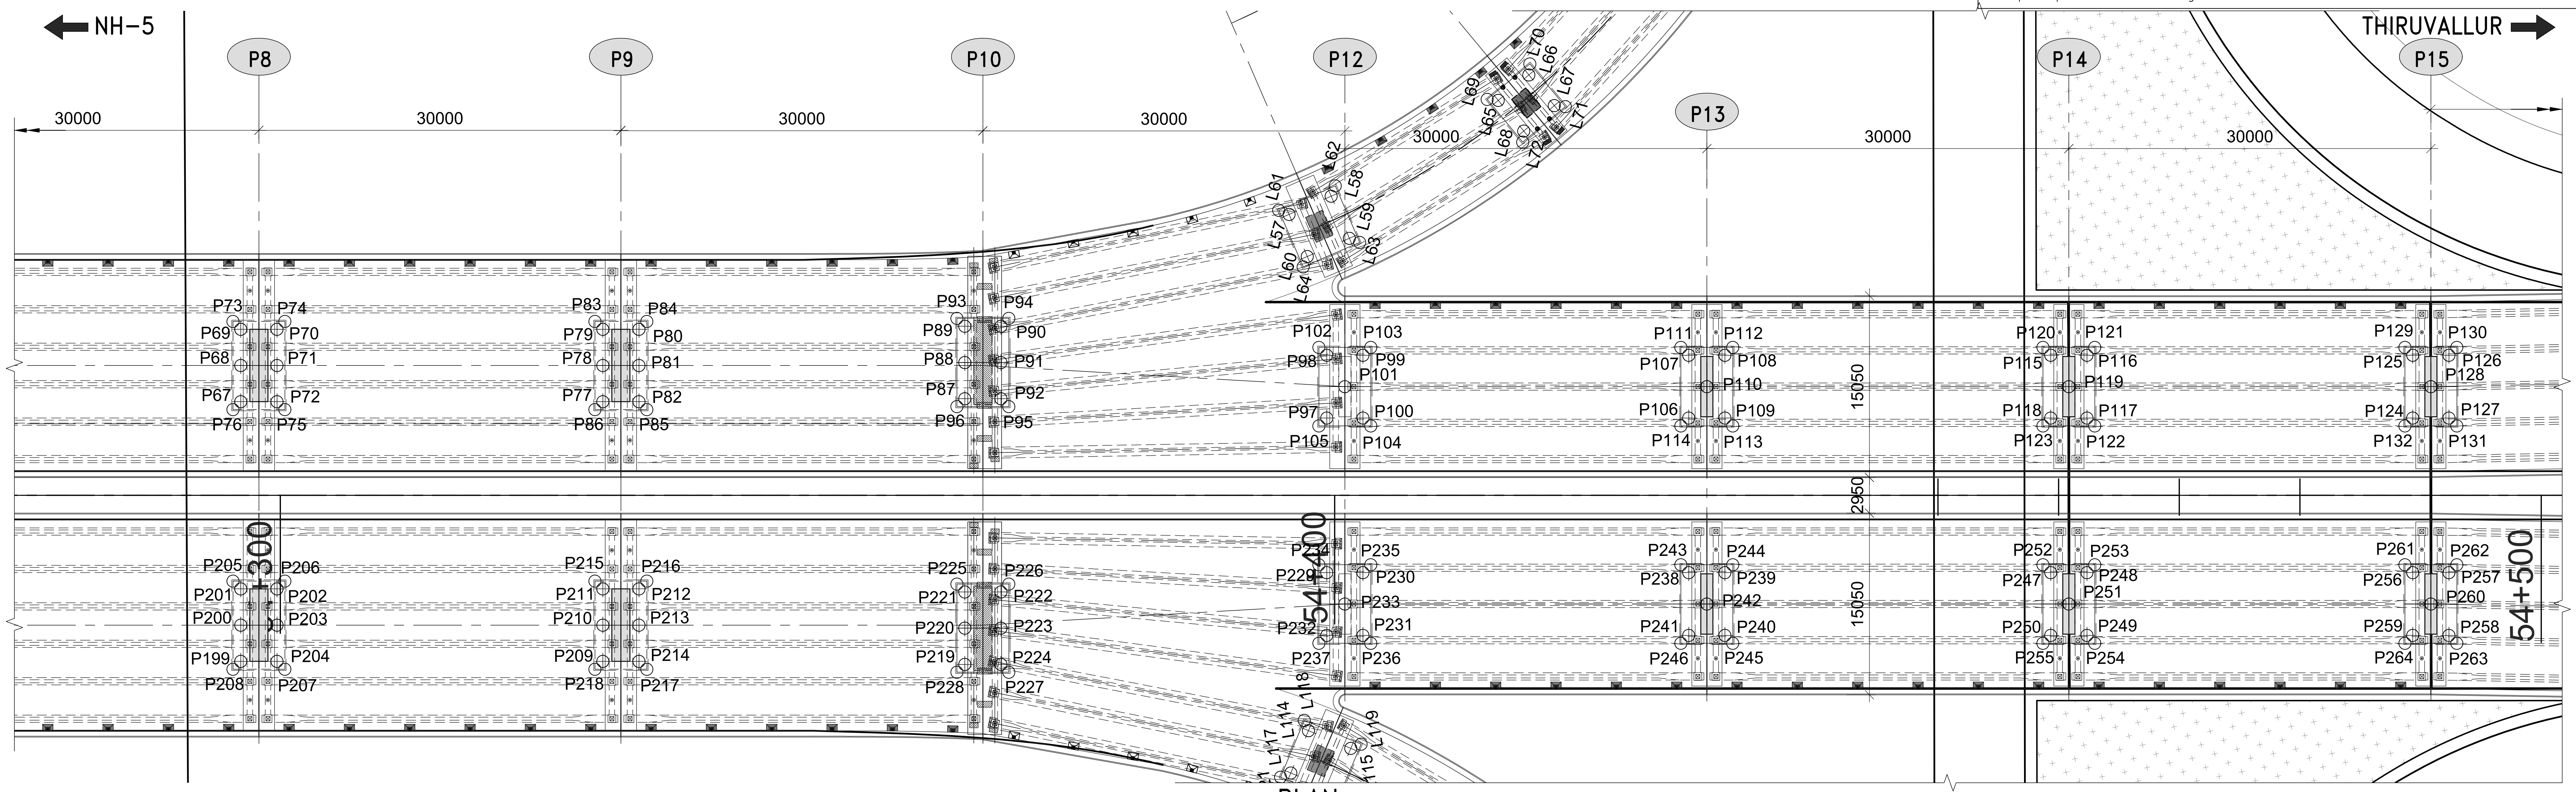
NH-5
THIRUVALLUR
P8
P9
P10
P12
P13
P14
P15
30000
15050
2950
54+300
54+400
54+500
P67 P68 P69 P70 P71 P72 P73 P74 P75 P76
P77 P78 P79 P80 P81 P82 P83 P84 P85 P86
P87 P88 P89 P90 P91 P92 P93 P94 P95 P96
P97 P98 P99 P100 P101 P102 P103 P104 P105
P106 P107 P108 P109 P110 P111 P112 P113 P114
P115 P116 P117 P118 P119 P120 P121 P122 P123
P124 P125 P126 P127 P128 P129 P130 P131 P132
P199 P200 P201 P202 P203 P204 P205 P206 P207 P208
P209 P210 P211 P212 P213 P214 P215 P216 P217 P218
P219 P220 P221 P222 P223 P224 P225 P226 P227 P228
P229 P230 P231 P232 P233 P234 P235 P236 P237
P238 P239 P240 P241 P242 P243 P244 P245 P246
P247 P248 P249 P250 P251 P252 P253 P254 P255
P256 P257 P258 P259 P260 P261 P262 P263 P264
L57 L58 L59 L60 L61 L62 L63 L64 L65 L66 L67 L68 L69 L70 L71 L72
L114 L115 L117 L118 L119

PLAN

LHS CARRIAGE WAY COORDINATES

PIER	POINTS	EASTING (X)	NORTHING (Y)
P8	P67	385955.348	1452215.981
	P68	385958.288	1452215.383
	P69	385961.228	1452214.786
	P70	385960.63	1452211.846
	P71	385957.69	1452212.444
	P72	385954.75	1452213.041
	P73	385961.994	1452215.293
	P74	385961.138	1452211.079
	P75	385953.984	1452212.534
	P76	385954.841	1452216.748
P9	P77	385949.371	1452186.582
	P78	385952.311	1452185.985
	P79	385955.251	1452185.387
	P80	385954.653	1452182.447
	P81	385951.713	1452183.045
	P82	385948.773	1452183.643
	P83	385956.017	1452185.895
	P84	385955.161	1452181.681
	P85	385948.007	1452183.135
	P86	385948.864	1452187.349
P10	P87	385943.639	1452157.134
	P88	385946.579	1452156.536
	P89	385949.519	1452155.939
	P90	385948.921	1452152.999
	P91	385945.981	1452153.597
	P92	385943.042	1452154.194
	P93	385950.285	1452156.446
	P94	385949.429	1452152.232
	P95	385942.275	1452153.687
	P96	385943.132	1452157.901
P12	P97	385936.094	1452128.054
	P98	385941.19	1452127.018
	P99	385940.592	1452124.078
	P100	385935.497	1452125.114
	P101	385938.343	1452126.066
	P102	385941.957	1452127.526
	P103	385941.1	1452123.312
	P104	385934.73	1452124.607
	P105	385935.587	1452128.821

LHS CARRIAGE WAY COORDINATES

PIER	POINTS	EASTING (X)	NORTHING (Y)
P13	P106	385930.117	1452098.656
	P107	385935.213	1452097.62
	P108	385934.615	1452094.68
	P109	385929.52	1452095.716
	P110	385932.366	1452096.668
	P111	385935.98	1452098.127
	P112	385935.123	1452093.913
	P113	385928.753	1452095.208
	P114	385929.61	1452099.422
P14	P115	385929.236	1452068.221
	P116	385928.639	1452065.281
	P117	385923.543	1452066.317
	P118	385924.14	1452069.257
	P119	385926.39	1452067.269
	P120	385930.003	1452068.729
	P121	385929.146	1452064.515
	P122	385922.776	1452065.81
	P123	385923.633	1452070.024
P15	P124	385918.164	1452039.859
	P125	385923.259	1452038.823
	P126	385922.662	1452035.883
	P127	385917.566	1452036.919
	P128	385920.413	1452037.871
	P129	385924.026	1452039.33
	P130	385923.169	1452035.116
	P131	385916.799	1452036.411
	P132	385917.656	1452040.625

RHS CARRIAGE WAY COORDINATES

PIER	POINTS	EASTING (X)	NORTHING (Y)
P8	P199	385934.279	1452220.265
	P200	385937.219	1452219.667
	P201	385940.159	1452219.069
	P202	385939.561	1452216.129
	P203	385936.621	1452216.727
	P204	385933.681	1452217.325
	P205	385940.925	1452219.577
	P206	385940.069	1452215.363
	P207	385932.915	1452216.817
	P208	385933.772	1452221.031
P9	P209	385928.302	1452190.866
	P210	385931.242	1452190.268
	P211	385934.182	1452189.671
	P212	385933.584	1452186.731
	P213	385930.644	1452187.328
	P214	385927.704	1452187.926
	P215	385934.948	1452190.178
	P216	385934.092	1452185.964
	P217	385926.938	1452187.419
	P218	385927.795	1452191.632
P10	P219	385922.08	1452161.517
	P220	385925.02	1452160.919
	P221	385927.96	1452160.322
	P222	385927.362	1452157.382
	P223	385924.422	1452157.98
	P224	385921.483	1452158.577
	P225	385928.726	1452160.829
	P226	385927.87	1452156.615
	P227	385920.716	1452158.07
	P228	385921.573	1452162.284
P12	P229	385923.551	1452130.604
	P230	385922.953	1452127.665
	P231	385917.858	1452128.701
	P232	385918.455	1452131.64
	P233	385920.704	1452129.653
	P234	385924.317	1452131.112
	P235	385923.461	1452126.898
	P236	385917.091	1452128.193
	P237	385917.948	1452132.407

RHS CARRIAGE WAY COORDINATES

PIER	POINTS	EASTING (X)	NORTHING (Y)
P13	P238	385917.574	1452101.206
	P239	385916.976	1452098.266
	P240	385911.881	1452099.302
	P241	385912.478	1452102.242
	P242	385914.727	1452100.254
	P243	385918.34	1452101.713
	P244	385917.484	1452097.5
	P245	385911.114	1452098.795
	P246	385911.971	1452103.008
P14	P247	385911.597	1452071.807
	P248	385910.999	1452068.867
	P249	385905.904	1452069.903
	P250	385906.501	1452072.843
	P251	385908.75	1452070.855
	P252	385912.364	1452072.315
	P253	385911.507	1452068.101
	P254	385905.137	1452069.396
	P255	385905.994	1452073.61
P15	P256	385905.62	1452042.409
	P257	385905.022	1452039.469
	P258	385899.927	1452040.505
	P259	385900.524	1452043.445
	P260	385902.773	1452041.457
	P261	385906.387	1452042.916
	P262	385905.53	1452038.702
	P263	385899.16	1452039.997
	P264	385900.017	1452044.211

REFERENCE DRAWING:–

1. GENERAL ARRANGEMENT DRAWING FOR INTERCHANGE AT CH: 57+542 - O24087-C-RP-MB-GA-8330

NOTES:

1. ALL DIMENSIONS ARE IN MILLIMETERS ,LEVELS AND CHAINAGES ARE IN METERS. UNLESS OTHERWISE MENTIONED.
2. DIMENSIONS ARE NOT TO BE SCALED, ONLY WRITTEN DIMENSIONS SHALL BE FOLLOWED.

THIS DRAWING SHALL BE READ IN CONJUNCTION WITH DRAWING NO. O24087-C-RP-MB-GA-8330

REV	DATE	DESCRIPTION	DESIGNED	DRAWN	CHECKED	APPROVED
RB	22.10.25	REVISED BASED ON SITE CONDITION	SRR	SR	ARS	NKC
RA	20.08.25	FOR APPROVAL	SRR	SRA	ARS	NKC

CLIENT :
TNRIDC
TAMILNADU ROAD INFRASTRUCTURE
DEVELOPMENT CORPORATION

AUTHORITY'S ENGINEER :
THEME ENGINEERING
SERVICE PVT. LTD.,

PROOF CONSULTANT :
ASIA INFRASTRUCTURE
ADVISORY SERVICES
PRIVATE LIMITED

SAFETY CONSULTANT :
ALMONDZ GLOBAL INFRA
- CONSULTANT LIMITED
(A wholly owned Subsidiary of AGSL)

PROJECT :
FORMATION OF NEW SIX LANE ROAD FROM THIRUVALLUR BYPASS (DESIGN CHAINAGE: CH 47+800) TO VENGATHUR (DESIGN CHAINAGE: CH 58+200) WITH PAVED SHOULDERS AND TWO LANE SERVICE ROAD ON BOTH SIDES IN SECTION-3 OF CHENNAI PERIPHERAL RING ROAD PROJECT UNDER PACKAGE-3 ON ENGINEERING, PROCUREMENT AND CONSTRUCTION (EPC) MODE INCLUDING MAINTENANCE FOR 7 YEARS.

CONTRACTOR :
L&T Construction
Transportation Infrastructure

DESIGN CONSULTANT :
L&T Construction
Transportation Infrastructure, EDRC

AUTHORITY'S ENGINEER
PROOF CONSULTANT
DESIGN DIRECTOR

JOB No. : O24087-C-RP

DESIGNED	SRR	
DRAWN	SRA	S Ranjitha
CHECKED	ARS	M.Gainom
APPROVED	NKC	NKC
DATE	SCALE	
20.08.2025		

TITLE : INTERCHANGE AT CH:54+281

FOUNDATION LAYOUT FOR
INTERCHANGE - MAIN CARRIAGE WAY

REV: RB
SIZE: A2

DRAWING NO :
O24087-C-RP-MB-NU-8390

SHEET: 02 OF 04

Cad File No: D:\CPRR-2\STRUCTURES\INTERCHANGE_MJB\COORDINATES\ O24087-C-RP-MB-NU-8390-REV.C-FOUNDATION LAYOUT.dwg

Plot Date: 27 October, 2025 - 12:10 PM

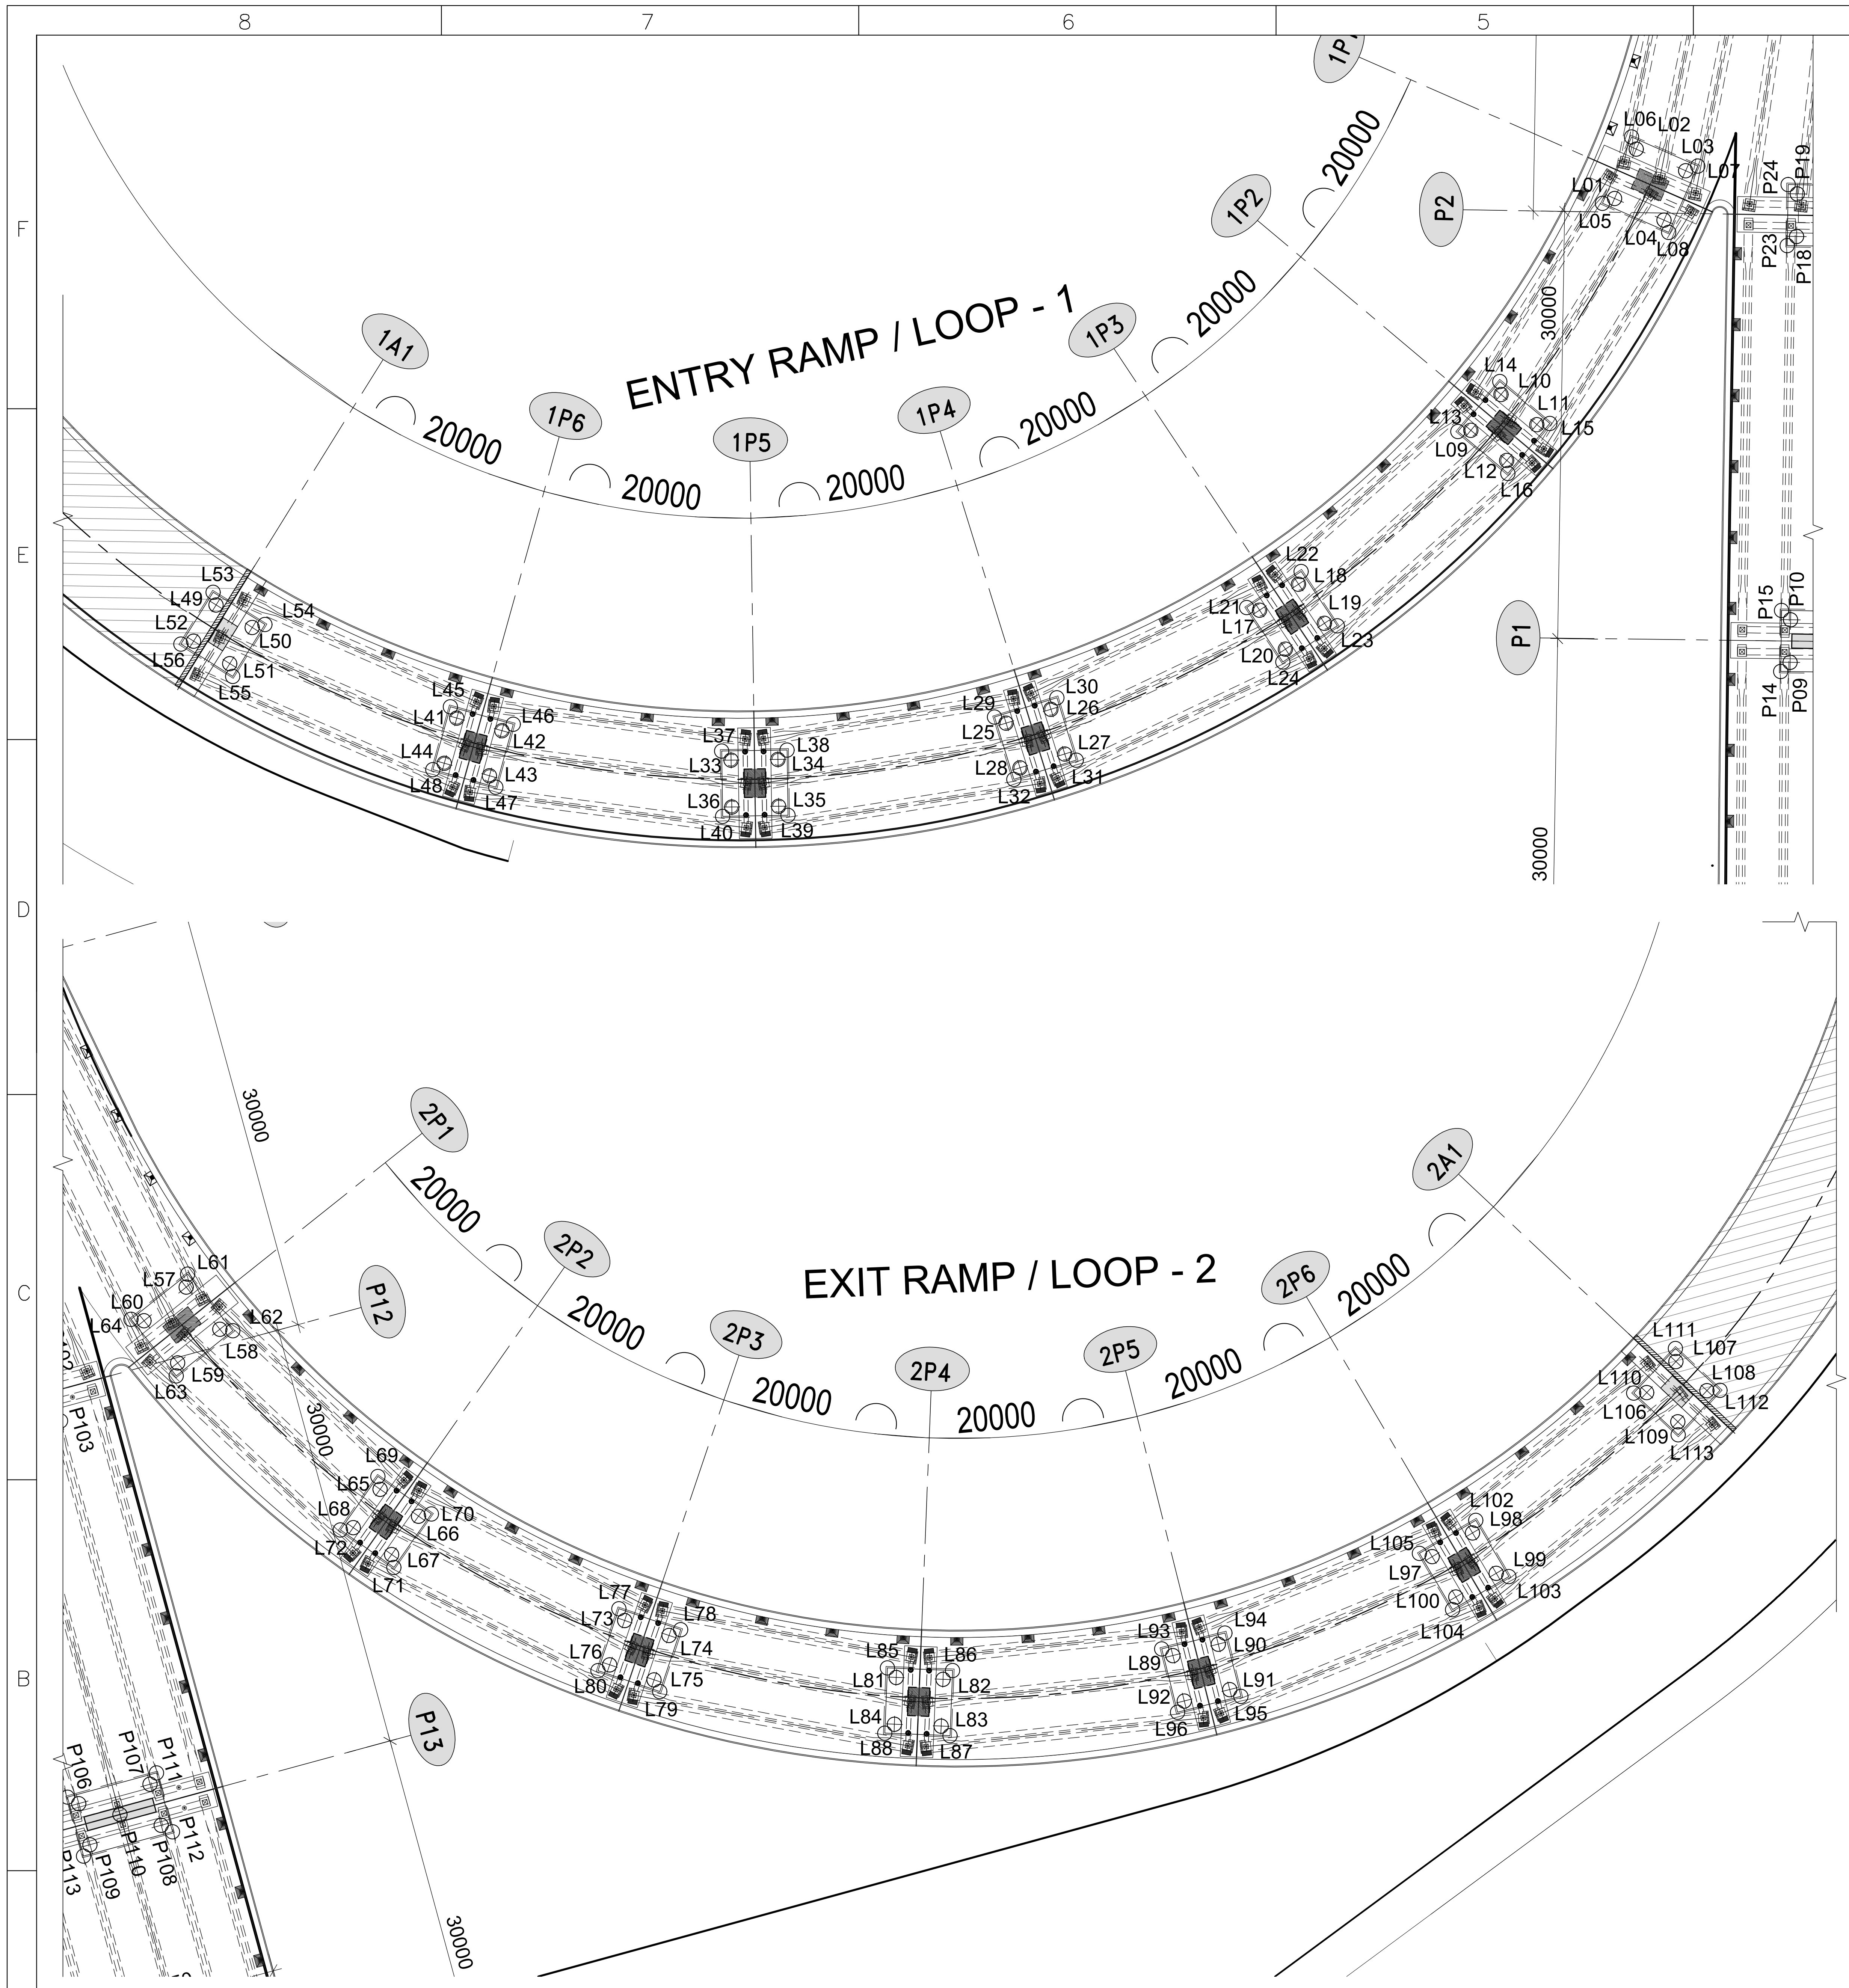
ENTRY RAMP / LOOP - 1
1A1
1P6
1P5
1P4
1P3
1P2
1P1
P1
P2
20000
30000
L01 L02 L03 L04 L05 L06 L07 L08
L09 L10 L11 L12 L13 L14 L15 L16
L17 L18 L19 L20 L21 L22 L23 L24
L25 L26 L27 L28 L29 L30 L31 L32
L33 L34 L35 L36 L37 L38 L39 L40
L41 L42 L43 L44 L45 L46 L47 L48
L49 L50 L51 L52 L53 L54 L55 L56
P24 P19 P23 P18 P15 P10 P14 P09
EXIT RAMP / LOOP - 2
2P1
2P2
2P3
2P4
2P5
2P6
2A1
P12
P13
L57 L58 L59 L60 L61 L62 L63 L64
L65 L66 L67 L68 L69 L70 L71 L72
L73 L74 L75 L76 L77 L78 L79 L80
L81 L82 L83 L84 L85 L86 L87 L88
L89 L90 L91 L92 L93 L94 L95 L96
L97 L98 L99 L100 L102 L103 L104 L105
L106 L107 L108 L109 L110 L111 L112 L113
P103 P106 P107 P111 P112 P113 P109 P110 P108

PLAN

LOOP-1 COORDINATES

PIER	POINTS	EASTING (X)	NORTHING (Y)
1P1	L01	386001.116	1452357.225
	L02	385998.979	1452354.083
	L03	385995.837	1452356.221
	L04	385997.975	1452359.362
	L05	386002.02	1452357.397
	L06	385999.151	1452353.18
	L07	385994.934	1452356.049
	L08	385997.803	1452360.266
1P2	L09	386014.066	1452371.426
	L10	386011.516	1452369.332
	L11	386009.421	1452371.881
	L12	386011.971	1452373.976
	L13	386014.981	1452371.337
	L14	386011.426	1452368.417
	L15	386008.506	1452371.971
	L16	386012.061	1452374.891
1P3	L17	386031.022	1452381.152
	L18	386027.985	1452379.861
	L19	386026.693	1452382.898
	L20	386029.73	1452384.189
	L21	386031.874	1452380.809
	L22	386027.641	1452379.009
	L23	386025.841	1452383.242
	L24	386030.074	1452385.042
1P4	L25	386050.031	1452385.705
	L26	386046.753	1452385.323
	L27	386046.37	1452388.6
	L28	386049.648	1452388.983
	L29	386050.752	1452385.135
	L30	386046.183	1452384.602
	L31	386045.649	1452389.171
	L32	386050.218	1452389.704
1P5	L33	386069.553	1452384.716
	L34	386066.3	1452385.273
	L35	386066.857	1452388.525
	L36	386070.11	1452387.969
	L37	386070.084	1452383.966
	L38	386065.55	1452384.742
	L39	386066.326	1452389.276
	L40	386070.86	1452388.5
1P6	L41	386088.005	1452378.265
	L42	386085.041	1452379.716
	L43	386086.492	1452382.68
	L44	386089.456	1452381.229
	L45	386088.303	1452377.395
	L46	386084.171	1452379.418
	L47	386086.194	1452383.549
	L48	386090.325	1452381.527
1A1	L49	386103.214	1452367.32
	L50	386101	1452369.345
	L51	386103.025	1452371.558
	L52	386105.238	1452369.534
	L53	386103.255	1452366.402
	L54	386100.082	1452369.304
	L55	386102.984	1452372.477
	L56	386106.157	1452369.574

LOOP-2 COORDINATES

PIER	POINTS	EASTING (X)	NORTHING (Y)
2P1	L57	385953.244	1452127.758
	L58	385954.025	1452124.039
	L59	385950.307	1452123.258
	L60	385949.525	1452126.976
	L61	385953.746	1452128.528
	L62	385954.795	1452123.537
	L63	385949.804	1452122.488
	L64	385948.755	1452127.479
2P2	L65	385959.038	1452108.887
	L66	385960.6	1452105.98
	L67	385957.693	1452104.419
	L68	385956.131	1452107.326
	L69	385959.303	1452109.767
	L70	385961.48	1452105.715
	L71	385957.428	1452103.538
	L72	385955.251	1452107.591
2P3	L73	385970.264	1452092.885
	L74	385972.581	1452090.535
	L75	385970.232	1452088.218
	L76	385967.914	1452090.567
	L77	385970.27	1452093.804
	L78	385973.5	1452090.529
	L79	385970.226	1452087.299
	L80	385966.995	1452090.573
2P4	L81	385985.544	1452080.695
	L82	385988.43	1452079.094
	L83	385986.829	1452076.208
	L84	385983.943	1452077.809
	L85	385985.291	1452081.578
	L86	385989.314	1452079.347
	L87	385987.082	1452075.324
	L88	385983.06	1452077.556
2P5	L89	386003.641	1452073.306
	L90	386006.861	1452072.583
	L91	386006.138	1452069.363
	L92	386002.918	1452070.086
	L93	386003.149	1452074.082
	L94	386007.637	1452073.075
	L95	386006.63	1452068.586
	L96	386002.142	1452069.594
2P6	L97	386023.087	1452071.316
	L98	386026.38	1452071.531
	L99	386026.594	1452068.238
	L100	386023.301	1452068.023
	L102	386026.986	1452072.221
	L103	386027.285	1452067.631
	L104	386022.694	1452067.333
	L105	386022.396	1452071.923
2A1	L106	386041.791	1452074.837
	L107	386044.608	1452075.868
	L108	386045.639	1452073.05
	L109	386042.821	1452072.02
	L110	386040.957	1452075.224
	L111	386044.995	1452076.702
	L112	386046.473	1452072.663
	L113	386042.434	1452071.186

REFERENCE DRAWING:-

1. GENERAL ARRANGEMENT DRAWING FOR INTERCHANGE AT CH: 57+542 - O24087-C-RP-MB-GA-8330

NOTES:

1. ALL DIMENSIONS ARE IN MILLIMETERS ,LEVELS AND CHAINAGES ARE IN METERS. UNLESS OTHERWISE MENTIONED.
2. DIMENSIONS ARE NOT TO BE SCALED, ONLY WRITTEN DIMENSIONS SHALL BE FOLLOWED.

THIS DRAWING SHALL BE READ IN CONJUNCTION WITH DRAWING NO. O24087-C-RP-MB-GA-8330

REV	DATE	DESCRIPTION	DESIGNED	DRAWN	CHECKED	APPROVED
RB	22.10.25	REVISED BASED ON SITE CONDITION	SRR	SR	ARS	NKC
RA	20.08.25	FOR APPROVAL	SRR	SRA	ARS	NKC

CLIENT :
TNRIDC
TAMILNADU ROAD INFRASTRUCTURE
DEVELOPMENT CORPORATION

AUTHORITY'S ENGINEER :
THEME ENGINEERING
SERVICE PVT. LTD.,

PROOF CONSULTANT :
ASIA INFRASTRUCTURE
ADVISORY SERVICES
PRIVATE LIMITED

SAFETY CONSULTANT :
ALMONDZ GLOBAL INFRA
- CONSULTANT LIMITED
(A wholly owned Subsidiary of AGSL)

PROJECT :
FORMATION OF NEW SIX LANE ROAD FROM THIRUVALLUR BYPASS (DESIGN CHAINAGE: CH 47+800) TO VENGATHUR (DESIGN CHAINAGE: CH 58+200) WITH PAVED SHOULDERS AND TWO LANE SERVICE ROAD ON BOTH SIDES IN SECTION-3 OF CHENNAI PERIPHERAL RING ROAD PROJECT UNDER PACKAGE-3 ON ENGINEERING, PROCUREMENT AND CONSTRUCTION (EPC) MODE INCLUDING MAINTENANCE FOR 7 YEARS.

CONTRACTOR :
L&T Construction
Transportation Infrastructure

DESIGN CONSULTANT :
L&T Construction
Transportation Infrastructure, EDRC

AUTHORITY'S ENGINEER

PROOF CONSULTANT

DESIGN DIRECTOR

DESIGN DIRECTOR

JOB No. : O24087-C-RP

DESIGNED	SRR	
DRAWN	SRA	S Ranjitha
CHECKED	ARS	
APPROVED	NKC	NKC
DATE	SCALE	
20.08.2025		

TITLE : INTERCHANGE AT CH:54+281
FOUNDATION LAYOUT FOR
INTERCHANGE - LOOP 1 & 2

REV: RB
SIZE: A2

DRAWING NO : O24087-C-RP-MB-NU-8390
SHEET: 03 OF 04

This drawing is the property of **TNRIDC and L&T Construction,Transportation Infrastructure** and must not be passed on to any person or body not authorised by us to receive it nor be copied or otherwise made use either in full or in part by suchperson or body without our prior permission in writing.

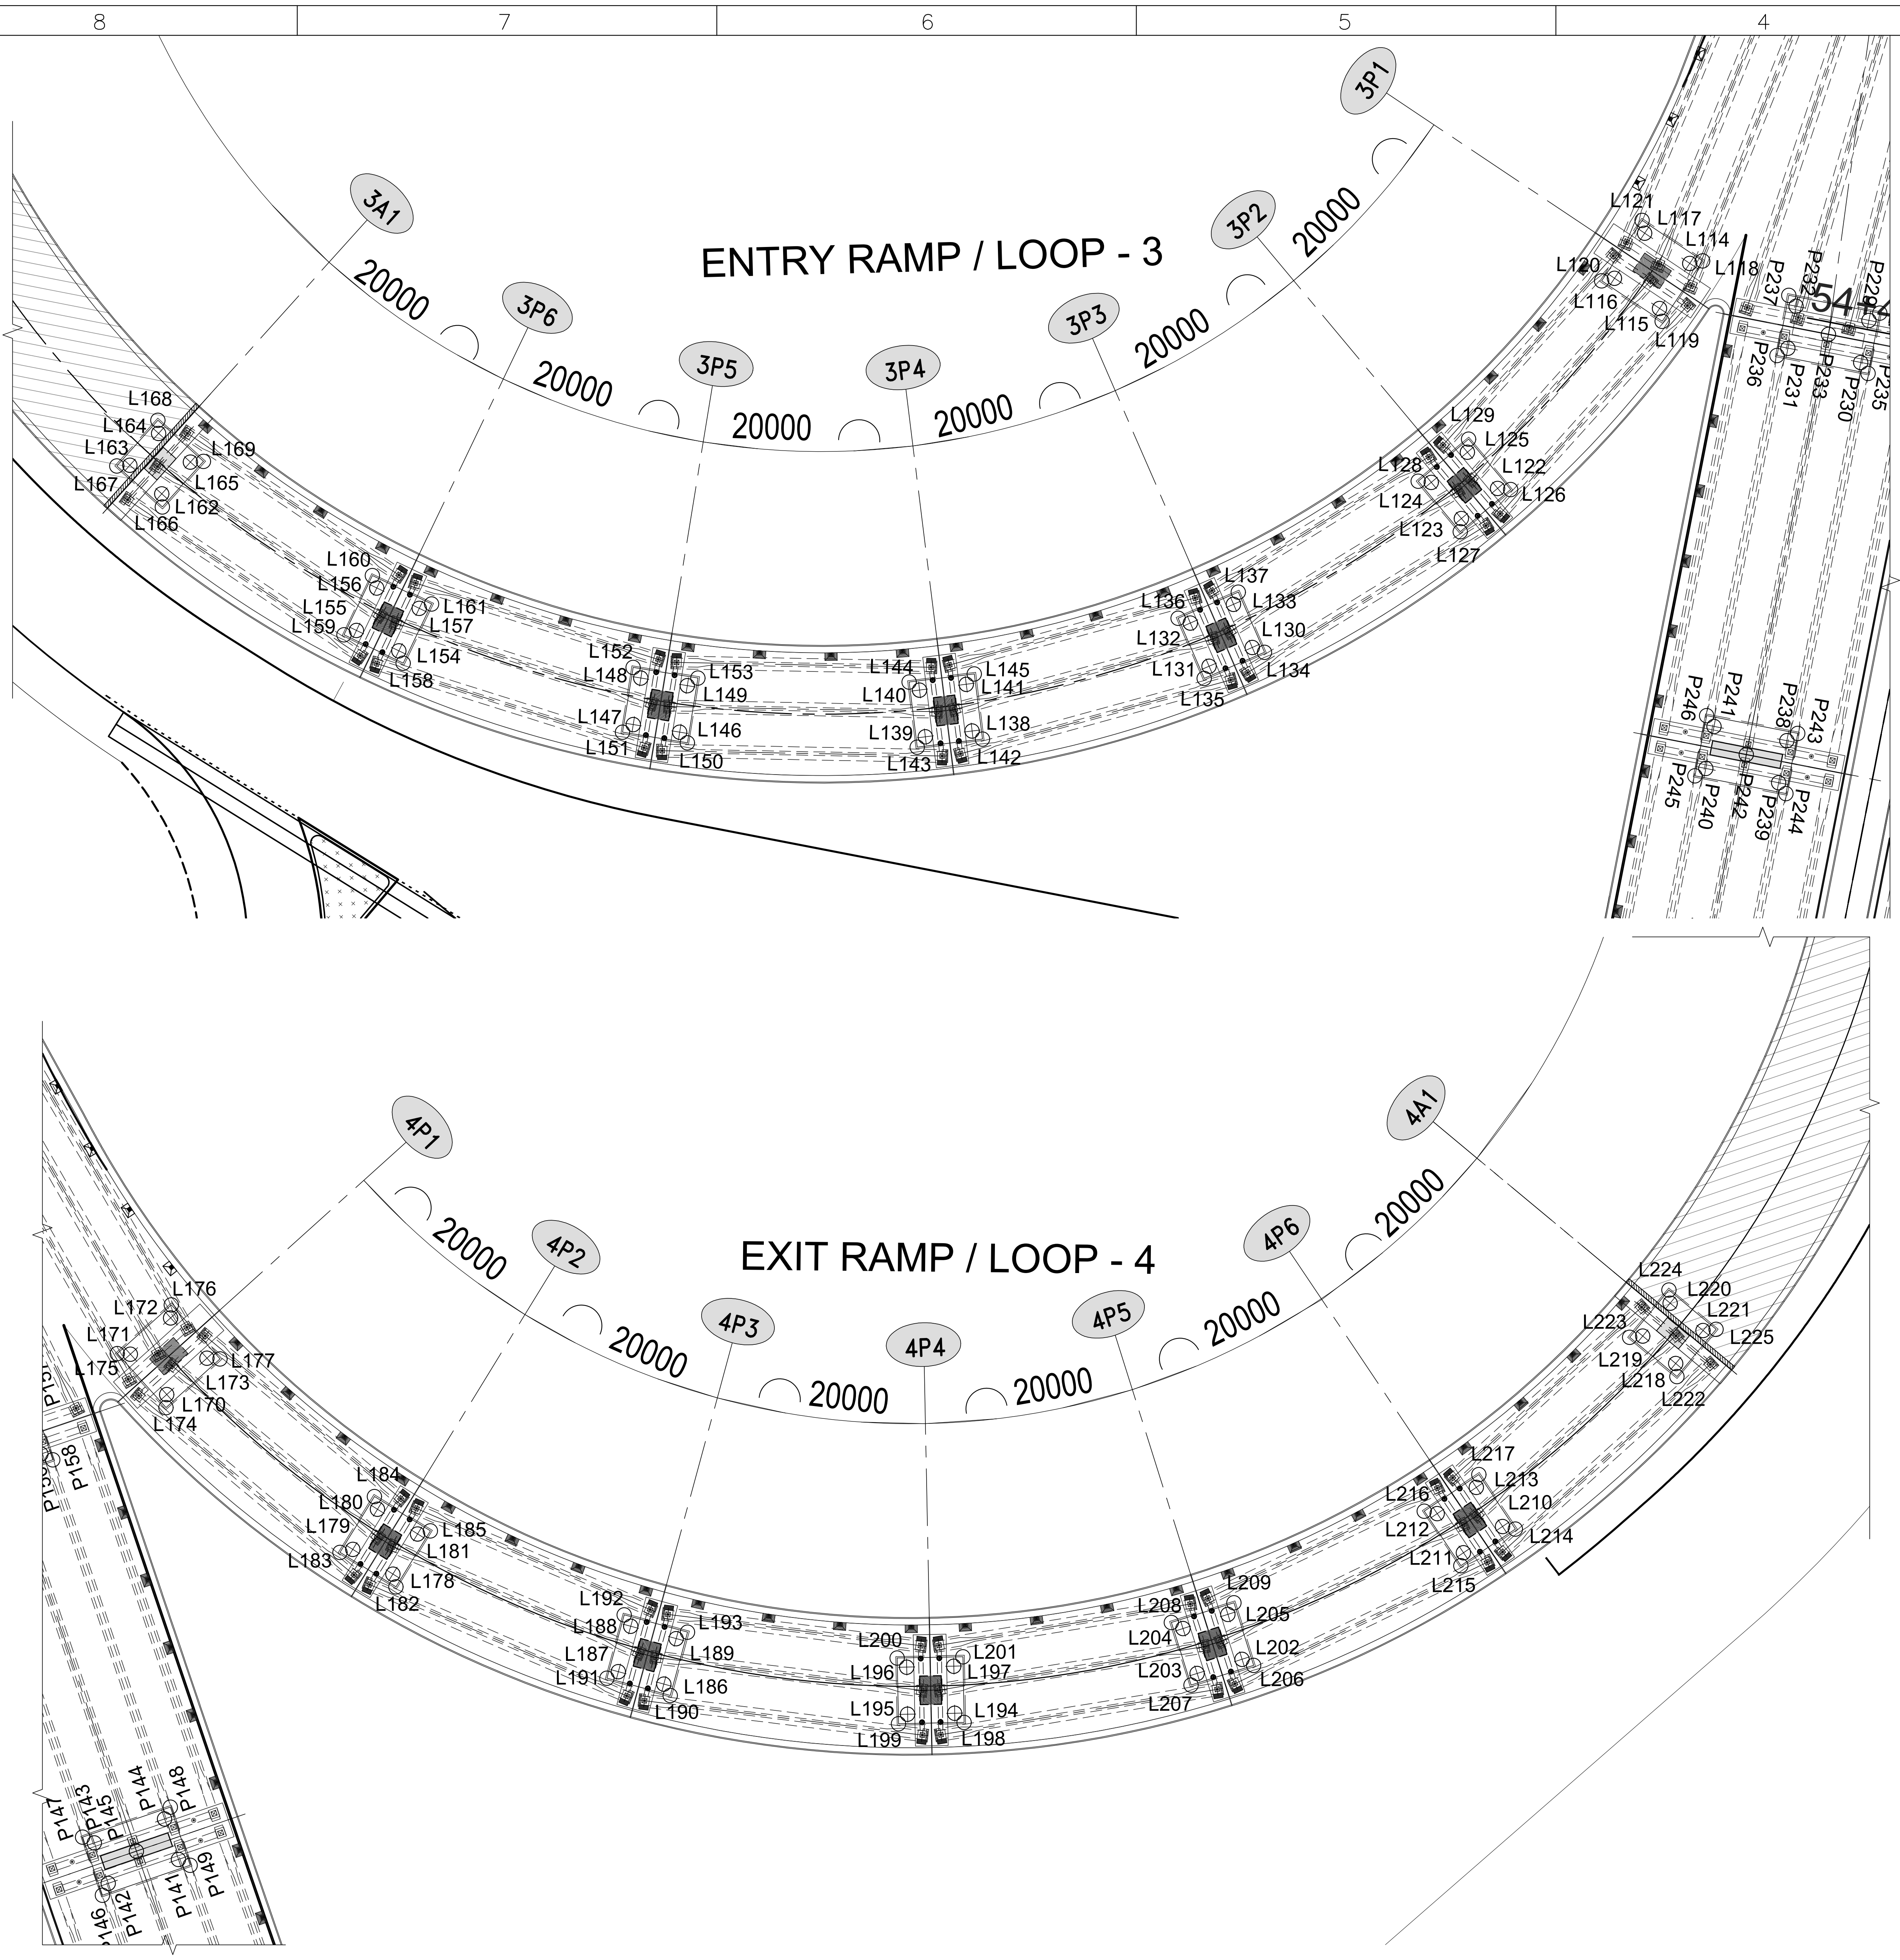
ENTRY RAMP / LOOP - 3
3P1
3P2
3P3
3P4
3P5
3P6
3A1
20000
L114 L115 L116 L117 L118 L119 L120 L121
L122 L123 L124 L125 L126 L127 L128 L129
L130 L131 L132 L133 L134 L135 L136 L137
L138 L139 L140 L141 L142 L143 L144 L145
L146 L147 L148 L149 L150 L151 L152 L153
L154 L155 L156 L157 L158 L159 L160 L161
L162 L163 L164 L165 L166 L167 L168 L169
P229 P230 P231 P232 P233 P235 P236 P237
P238 P239 P240 P241 P242 P243 P244 P245 P246
EXIT RAMP / LOOP - 4
4P1
4P2
4P3
4P4
4P5
4P6
4A1
L170 L171 L172 L173 L174 L175 L176 L177
L178 L179 L180 L181 L182 L183 L184 L185
L186 L187 L188 L189 L190 L191 L192 L193
L194 L195 L196 L197 L198 L199 L200 L201
L202 L203 L204 L205 L206 L207 L208 L209
L210 L211 L212 L213 L214 L215 L216 L217
L218 L219 L220 L221 L222 L223 L224 L225
P141 P142 P143 P144 P145 P146 P147 P148 P149 P158

PLAN

LOOP-3 COORDINATES

PIER	POINTS	EASTING (X)	NORTHING (Y)
3P1	L114	385911.026	1452134.696
	L115	385908.888	1452131.554
	L116	385905.747	1452133.692
	L117	385907.884	1452136.833
	L118	385911.929	1452134.868
	L119	385909.06	1452130.651
	L120	385904.844	1452133.52
	L121	385907.713	1452137.737
3P2	L122	385897.441	1452119.036
	L123	385894.891	1452116.941
	L124	385892.796	1452119.491
	L125	385895.346	1452121.586
	L126	385898.356	1452118.946
	L127	385894.801	1452116.026
	L128	385891.882	1452119.581
	L129	385895.436	1452122.501
3P3	L130	385880.168	1452108.02
	L131	385877.131	1452106.729
	L132	385875.84	1452109.766
	L133	385878.877	1452111.057
	L134	385881.021	1452107.676
	L135	385876.787	1452105.877
	L136	385874.988	1452110.11
	L137	385879.221	1452111.91
3P4	L138	385860.491	1452102.319
	L139	385857.213	1452101.937
	L140	385856.83	1452105.214
	L141	385860.108	1452105.597
	L142	385861.212	1452101.749
	L143	385856.643	1452101.216
	L144	385856.109	1452105.785
	L145	385860.678	1452106.318
3P5	L146	385840.004	1452102.395
	L147	385836.752	1452102.952
	L148	385837.308	1452106.205
	L149	385840.561	1452105.648
	L150	385840.535	1452101.645
	L151	385836.001	1452102.421
	L152	385836.777	1452106.955
	L153	385841.311	1452106.179
3P6	L154	385820.37	1452108.242
	L155	385817.406	1452109.693
	L156	385818.857	1452112.657
	L157	385821.821	1452111.206
	L158	385820.668	1452107.373
	L159	385816.536	1452109.395
	L160	385818.559	1452113.527
	L161	385822.69	1452111.504
3A1	L162	385803.837	1452119.365
	L163	385801.624	1452121.39
	L164	385803.649	1452123.603
	L165	385805.862	1452121.578
	L166	385803.878	1452118.446
	L167	385800.706	1452121.349
	L168	385803.608	1452124.521
	L169	385806.781	1452121.619

LOOP-4 COORDINATES

PIER	POINTS	EASTING (X)	NORTHING (Y)
4P1	L170	385956.561	1452367.651
	L171	385957.342	1452363.933
	L172	385953.624	1452363.151
	L173	385952.842	1452366.87
	L174	385957.064	1452368.421
	L175	385958.112	1452363.43
	L176	385953.121	1452362.382
	L177	385952.073	1452367.373
4P2	L178	385949.178	1452386.492
	L179	385950.739	1452383.584
	L180	385947.832	1452382.023
	L181	385946.271	1452384.931
	L182	385949.444	1452387.372
	L183	385951.62	1452383.319
	L184	385947.567	1452381.143
	L185	385945.391	1452385.196
4P3	L186	385936.642	1452402.694
	L187	385938.959	1452400.345
	L188	385936.609	1452398.028
	L189	385934.292	1452400.377
	L190	385936.648	1452403.614
	L191	385939.878	1452400.338
	L192	385936.603	1452397.108
	L193	385933.373	1452400.384
4P4	L194	385920.046	1452414.707
	L195	385922.932	1452413.105
	L196	385921.33	1452410.22
	L197	385918.445	1452411.821
	L198	385919.793	1452415.59
	L199	385923.815	1452413.358
	L200	385921.583	1452409.336
	L201	385917.561	1452411.568
4P5	L202	385900.738	1452421.555
	L203	385903.958	1452420.832
	L204	385903.235	1452417.612
	L205	385900.015	1452418.335
	L206	385900.246	1452422.331
	L207	385904.735	1452421.323
	L208	385903.727	1452416.835
	L209	385899.238	1452417.843
4P6	L210	385880.283	1452422.683
	L211	385883.576	1452422.897
	L212	385883.79	1452419.604
	L213	385880.496	1452419.39
	L214	385879.592	1452423.29
	L215	385884.182	1452423.588
	L216	385884.48	1452418.997
	L217	385879.89	1452418.7
4A1	L218	385864.055	1452418.904
	L219	385865.085	1452416.086
	L220	385862.267	1452415.056
	L221	385861.237	1452417.873
	L222	385864.442	1452419.737
	L223	385865.918	1452415.699
	L224	385861.88	1452414.222
	L225	385860.403	1452418.261

REFERENCE DRAWING:-

1. GENERAL ARRANGEMENT DRAWING FOR INTERCHANGE AT CH: 57+542 - O24087-C-RP-MB-GA-8330

NOTES:

1. ALL DIMENSIONS ARE IN MILLIMETERS ,LEVELS AND CHAINAGES ARE IN METERS. UNLESS OTHERWISE MENTIONED.
2. DIMENSIONS ARE NOT TO BE SCALED, ONLY WRITTEN DIMENSIONS SHALL BE FOLLOWED.

THIS DRAWING SHALL BE READ IN CONJUNCTION WITH DRAWING NO. O24087-C-RP-MB-GA-8330

REV	DATE	DESCRIPTION	DESIGNED	DRAWN	CHECKED	APPROVED
RB	22.10.25	REVISED BASED ON SITE CONDITION	SRR	SR	ARS	NKC
RA	20.08.25	FOR APPROVAL	SRR	SRA	ARS	NKC

CLIENT :
TNRIDC
TAMILNADU ROAD INFRASTRUCTURE
DEVELOPMENT CORPORATION

AUTHORITY'S ENGINEER :
THEME ENGINEERING
SERVICE PVT. LTD.,

PROOF CONSULTANT :
ASIA INFRASTRUCTURE
ADVISORY SERVICES
PRIVATE LIMITED

SAFETY CONSULTANT :
ALMONDZ GLOBAL INFRA
- CONSULTANT LIMITED
(A wholly owned Subsidiary of AGSL)

PROJECT :
FORMATION OF NEW SIX LANE ROAD FROM THIRUVALLUR BYPASS (DESIGN CHAINAGE: CH 47+800) TO VENGATHUR (DESIGN CHAINAGE: CH 58+200) WITH PAVED SHOULDERS AND TWO LANE SERVICE ROAD ON BOTH SIDES IN SECTION-3 OF CHENNAI PERIPHERAL RING ROAD PROJECT UNDER PACKAGE-3 ON ENGINEERING, PROCUREMENT AND CONSTRUCTION (EPC) MODE INCLUDING MAINTENANCE FOR 7 YEARS.

CONTRACTOR :
L&T Construction
Transportation Infrastructure

DESIGN CONSULTANT :
L&T Construction
Transportation Infrastructure, EDRC

AUTHORITY'S ENGINEER

ASIA INFRASTRUCTURE ADVISORY SERVICES (P) LTD.

PROOF CONSULTANT

L&T CONSTRUCTION CHENNAI
DESIGN DIRECTOR
TI - IC

DESIGN DIRECTOR

JOB No. : O24087-C-RP

DESIGNED	SRR	
DRAWN	SRA	S Ranjitha
CHECKED	ARS	
APPROVED	NKC	NKC
DATE	SCALE	
20.08.2025		

TITLE :
INTERCHANGE AT CH:54+281
FOUNDATION LAYOUT FOR
INTERCHANGE - LOOP 3 & 4

REV: RB
SIZE: A2

DRAWING NO :
O24087-C-RP-MB-NU-8390

SHEET:
04 OF 04

Cad File No: D:\CPRR-2\STRUCTURES\INTERCHANGE_MJB\COORDINATES\ O24087-C-RP-MB-NU-8390-REV.C-FOUNDATION LAYOUT.dwg

Plot Date: 27 October, 2025 - 12:10 PM